




千歳市柏陽5丁目1-3の内

附 近 見 取 図

設計概要


工 事 名 称	米山久邸 新築工事			
地 名 地 番	千歳市柏陽5丁目1－3の内			
住 居 表 示	千歳市柏陽5丁目1－3			
用 途 地 域	第1種低層住居専用地域			
防 火 指 定	法第22条区域			
構 造	木造軸組構法 平屋			
主 要 用 途	住宅			
敷 地 面 積	372.40	m ² (112.5 坪)		
	申請建物		合計	
建 築 面 積	43.68	m ² (13.19 坪)	113.68	m ² (34.34 坪)
延 床 面 積	34.99	m ² (10.57 坪)	140.99	m ² (42.59 坪)
容積対象床面積	34.99	m ²	140.99	m ²
建 蔽 率	30.53	% < 40 %		
容 積 率	37.86	% < 60 %		
最 高 高 さ	3,600	mm		
最 高 軒 高	3,259	mm		
備 考				

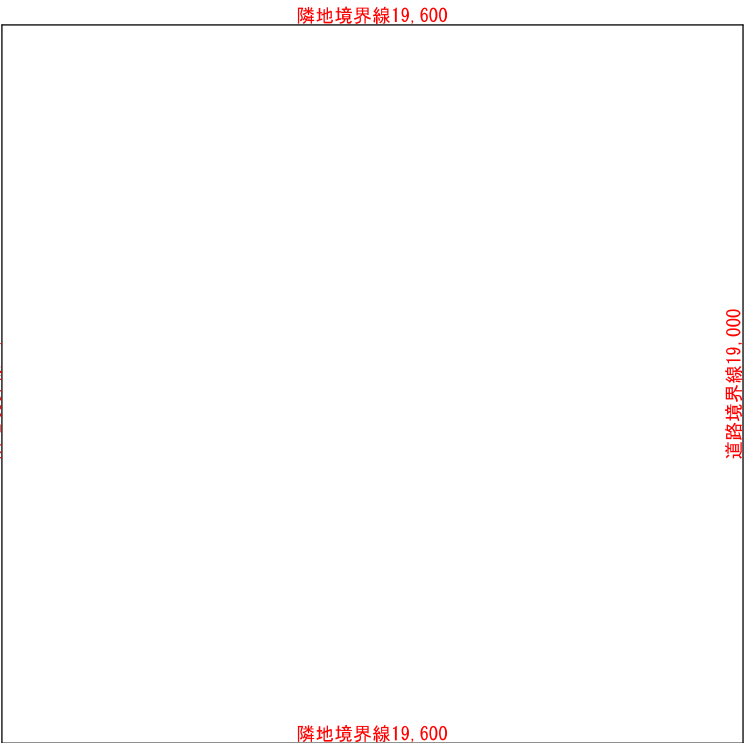

敷地求積図 1 : 200

	計 算 式	計
面積	19.600 × 19.000	372.400 m ²

- ・火を使用する設備またはその使用に際し、火災の発生の恐れのある設備の位置、構造は、火災予防条例の規定に従う
- ・給湯設備の転倒防止等については、平成12年建設省告示第1388号に定める方法による

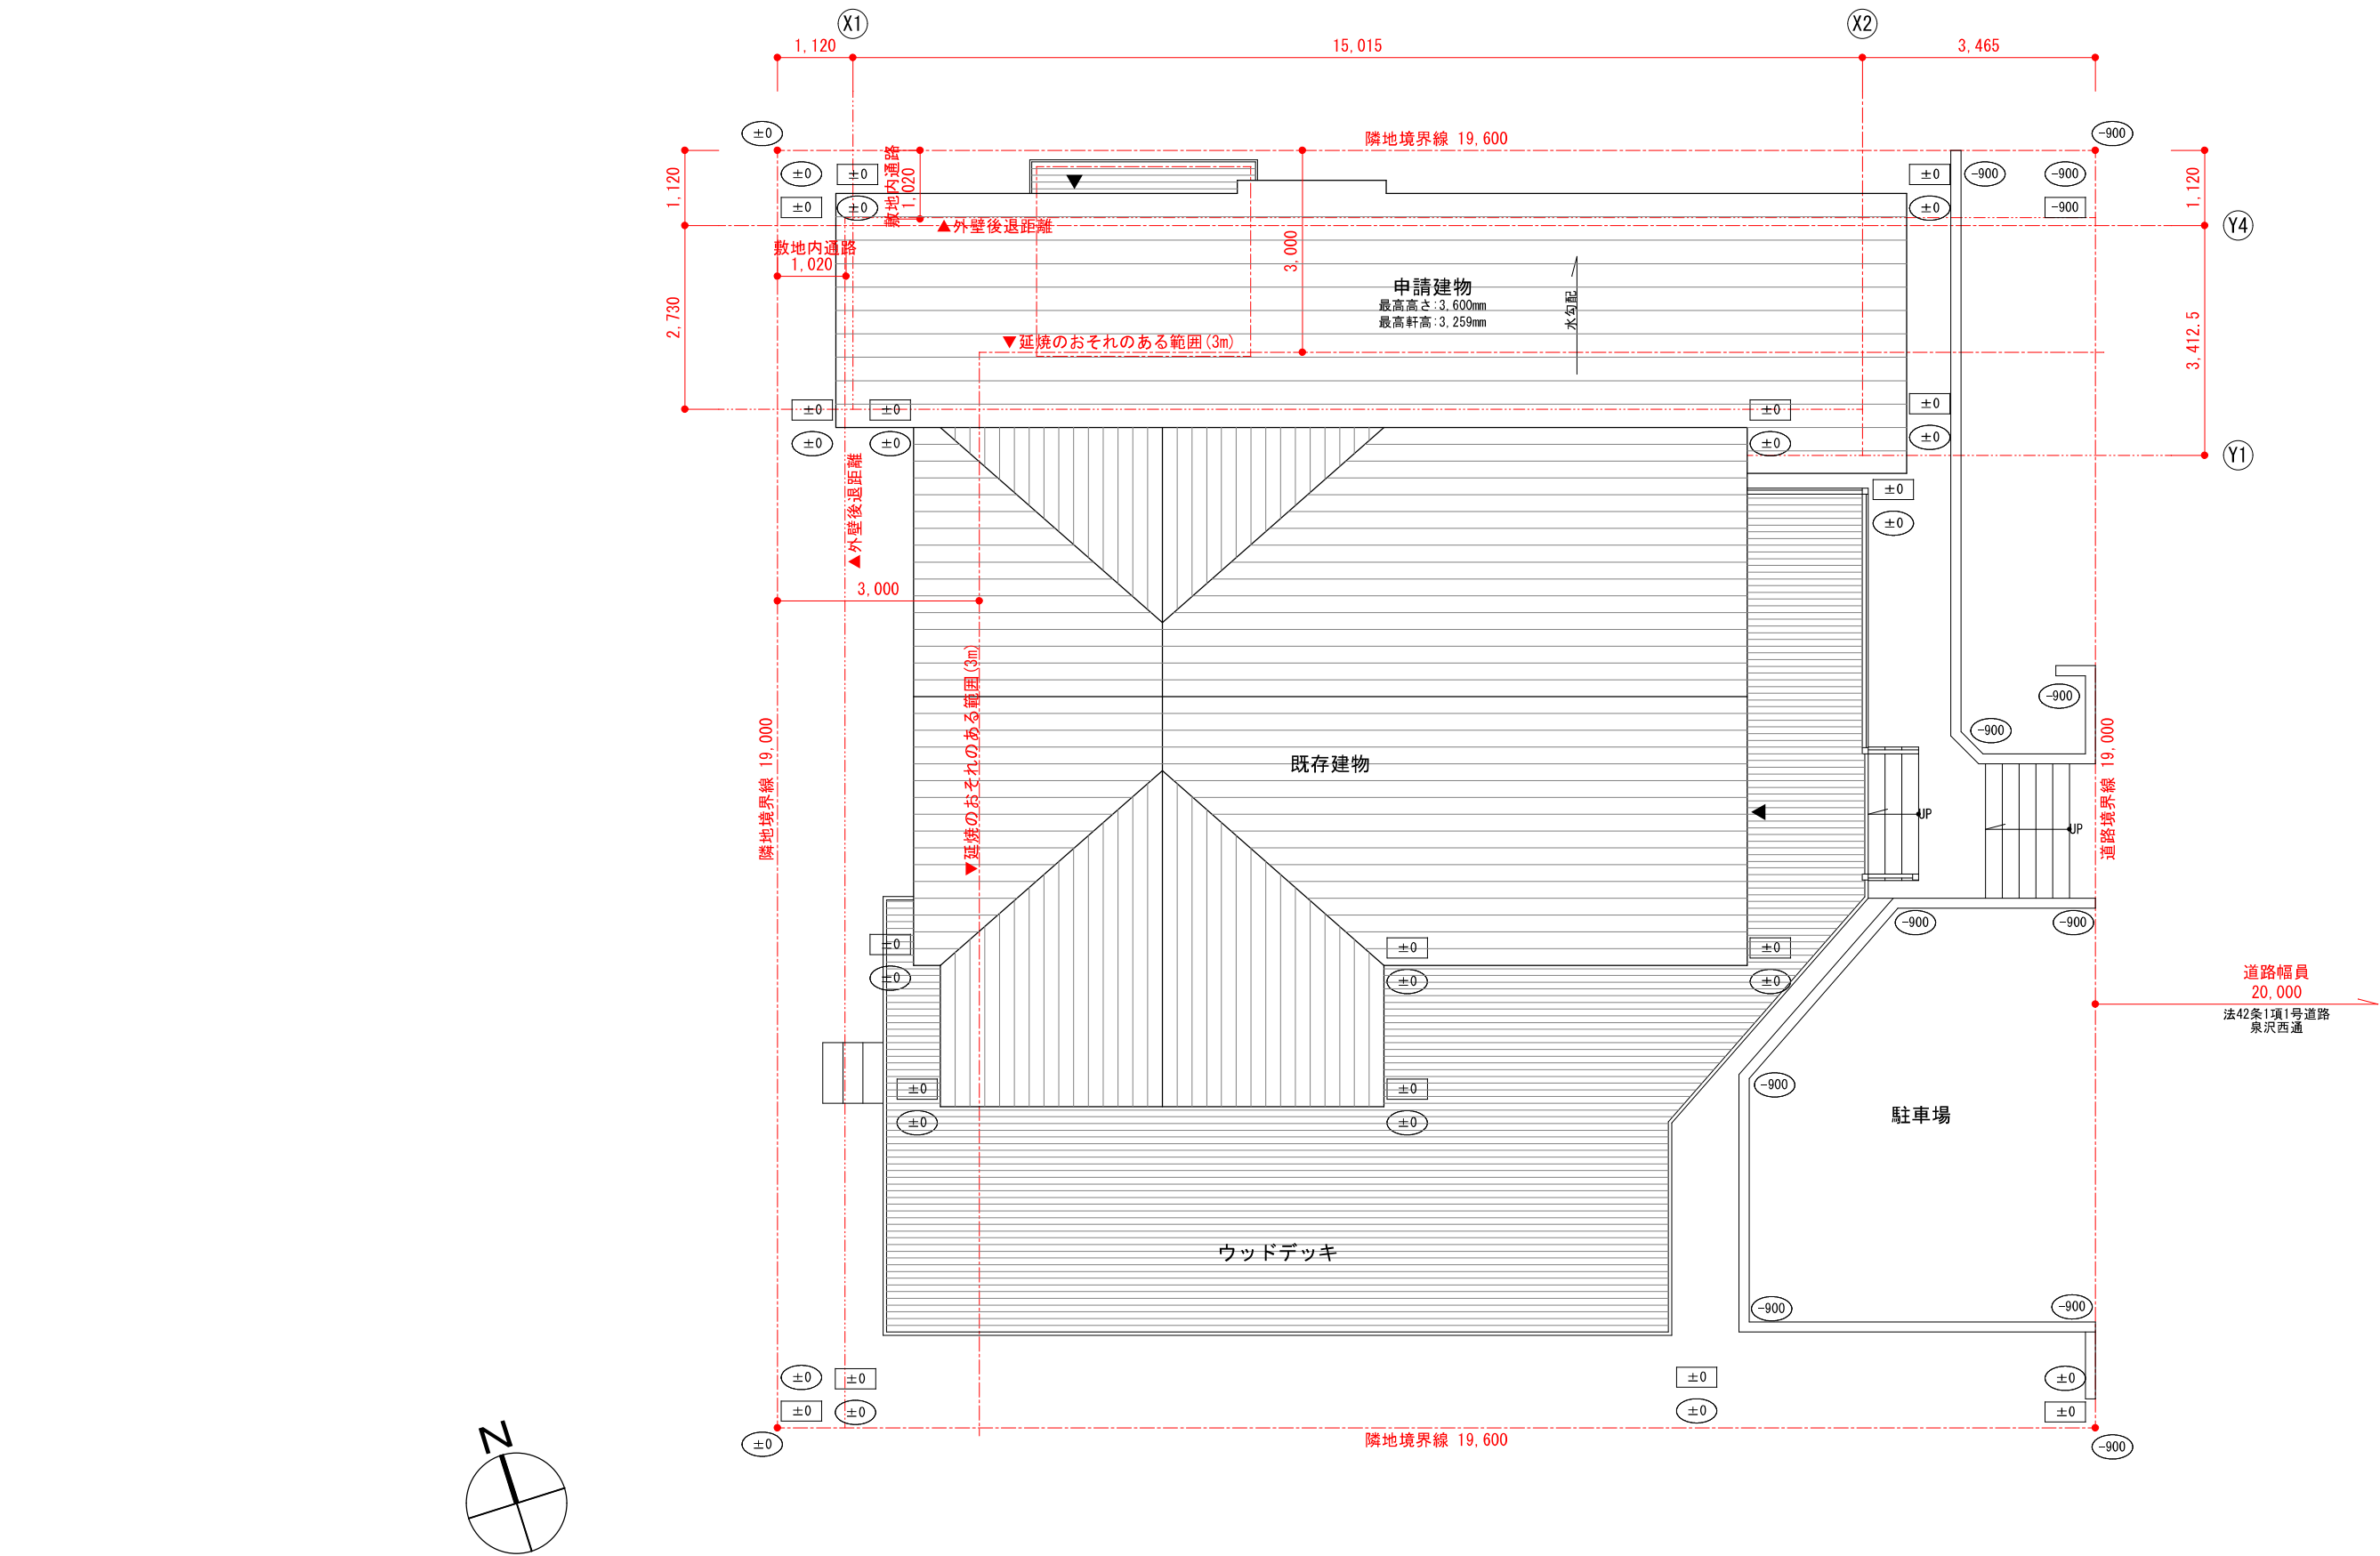

凡例	
±0	: 設計GL
±0	: 現況GL

- ・雨水は敷地内で処理する
- ・上下水道は関係法令に基づき設置する

Copyright(C) 2004- T-size All rights reserved.



北海道知事登録(石)第5048号
一級建築士事務所 **ディーサイズ**

一級建築士登録 第302819号
塚本高正

TITLE 千歳市柏陽5丁目1-3
米山久郎 新築工事

TYPE OF DRAWING
建築概要・配置図


SCALE
1/100

DATE
'23.05.31

DRAW
Takamasa TSUKAMOTO

DRAWING NO.
002

[illegible]


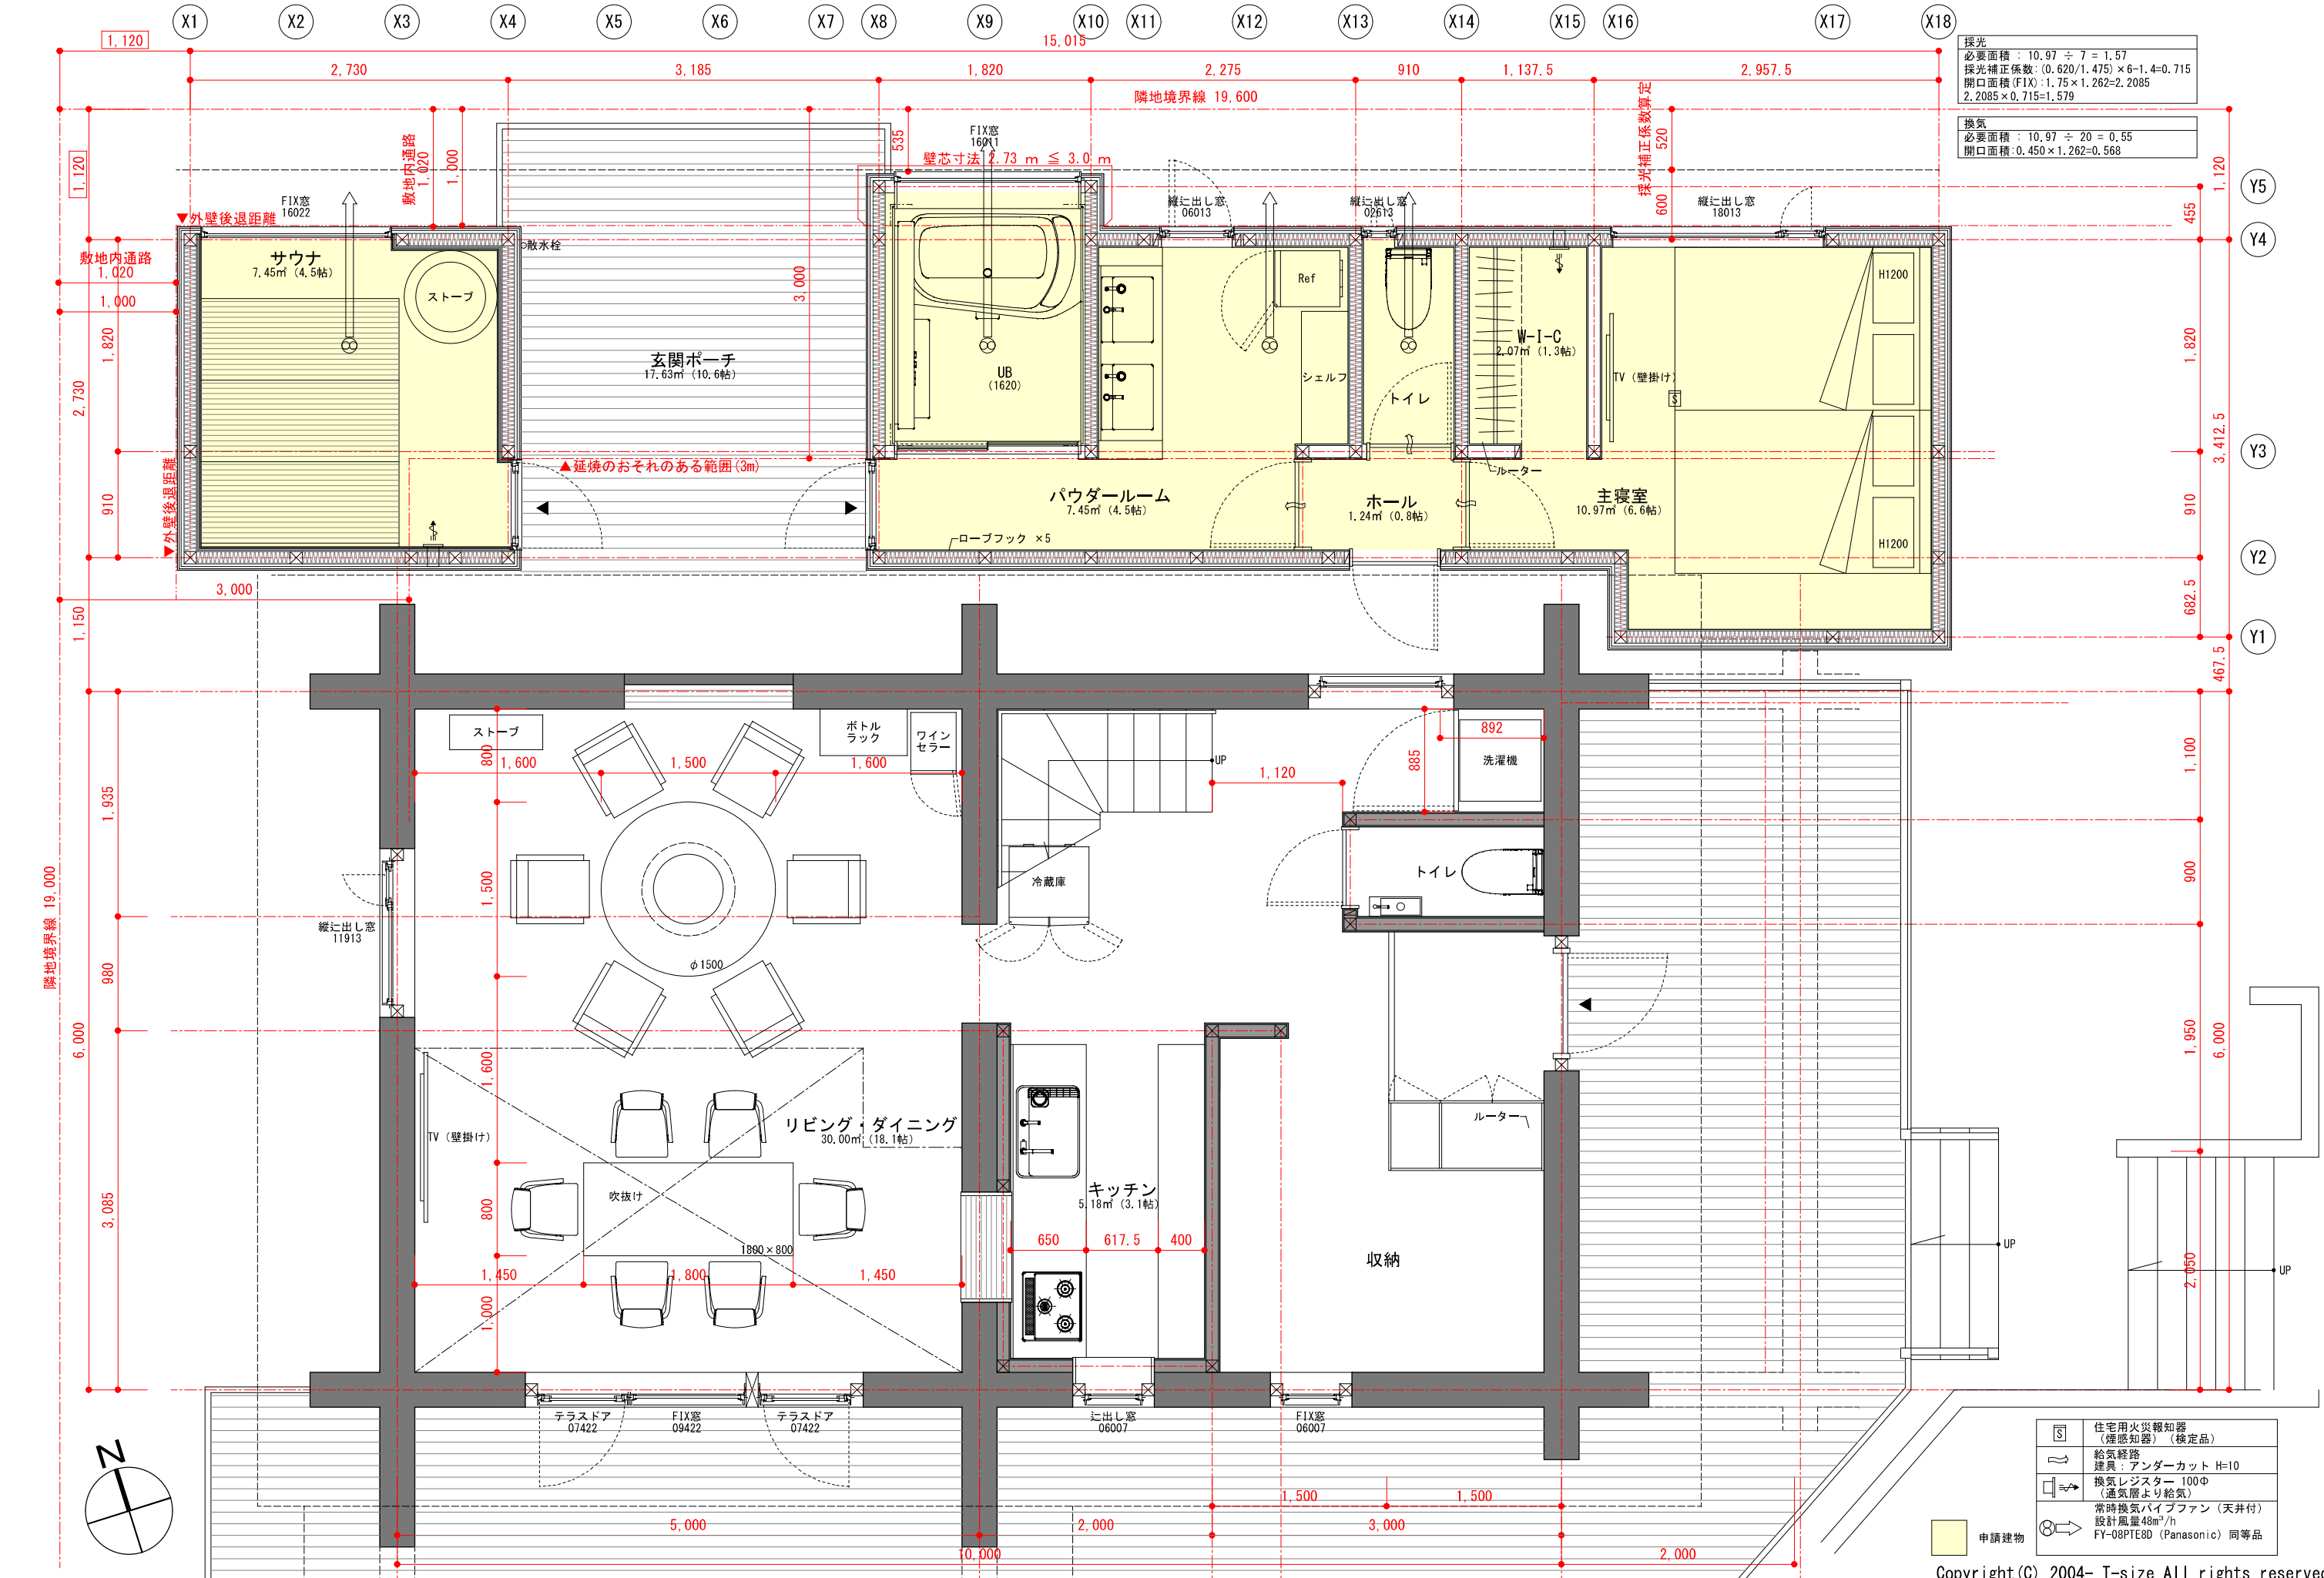



採光
必要面積 : 10.97 ÷ 7 = 1.57
採光補正係数 : (0.620/1.475) × 6-1.4=0.715
開口面積 (FIX) : 1.75 × 1.262=2.2085
2.2085 × 0.715=1.579

換気
必要面積 : 10.97 ÷ 20 = 0.55
開口面積 : 0.450 × 1.262=0.568

- 住宅用火災報知器 (煙感知器) (検定品)
- 給気経路 器具 : アンダーカット H=10
- 換気レジスター 100Φ (通気層より給気)
- 常時換気バイパスファン (天井付) 設計風量48m³/h FY-08PTE80 (Panasonic) 同等品


Copyright (C) 2004- T-size All rights reserved.

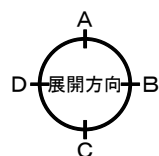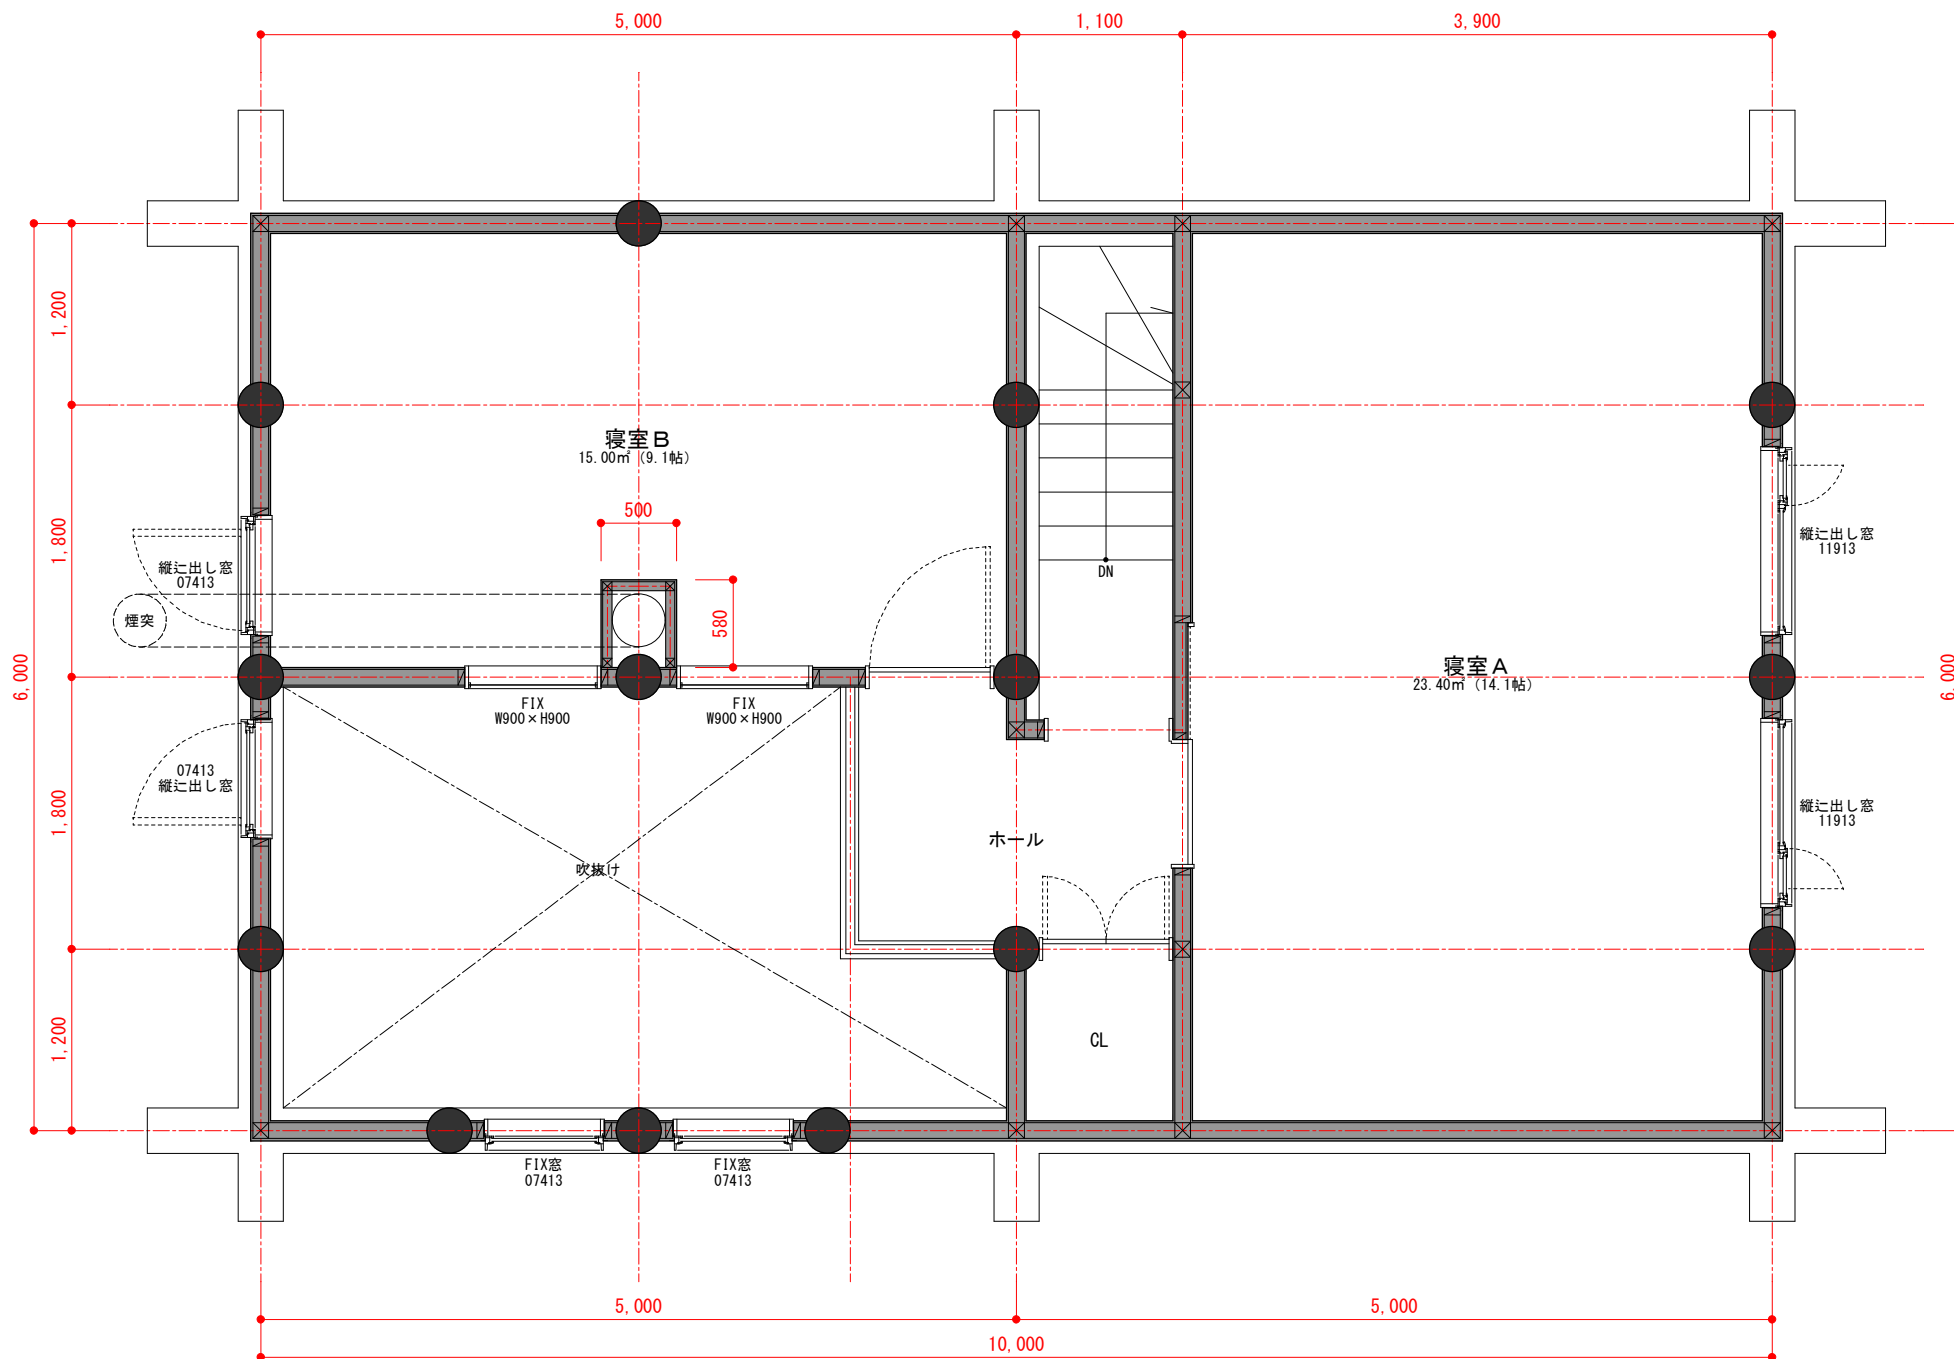

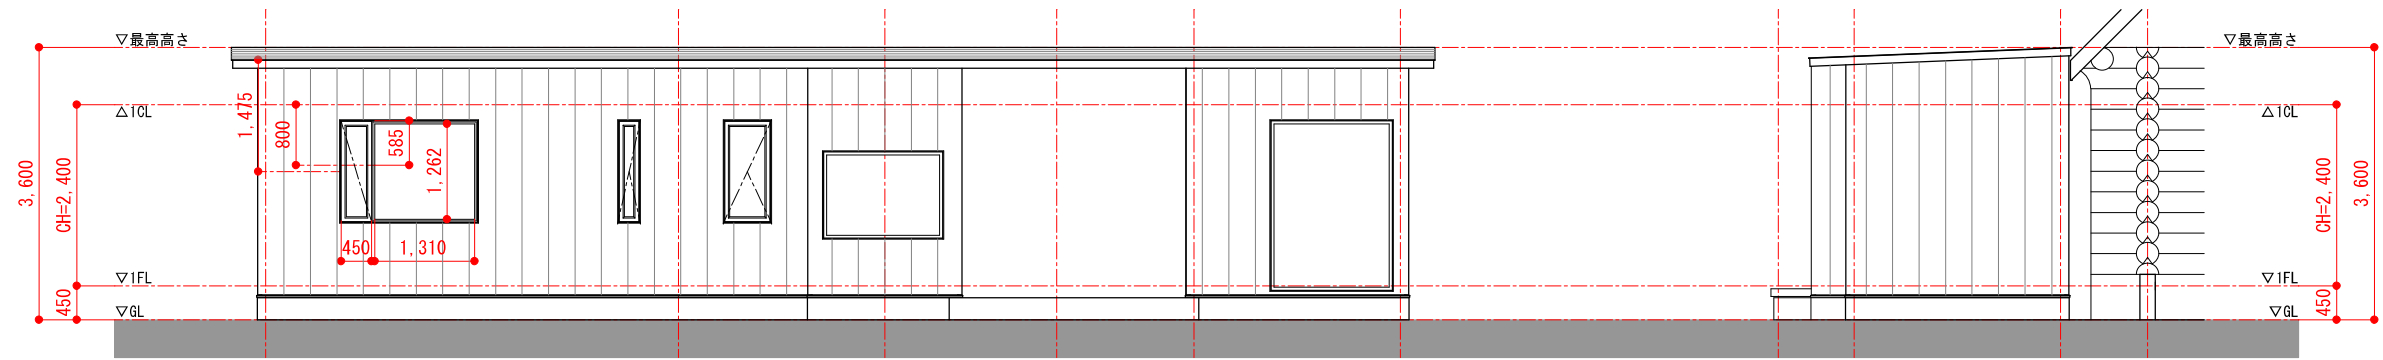


北側立面図 1 : 100


西側立面図 1 : 100

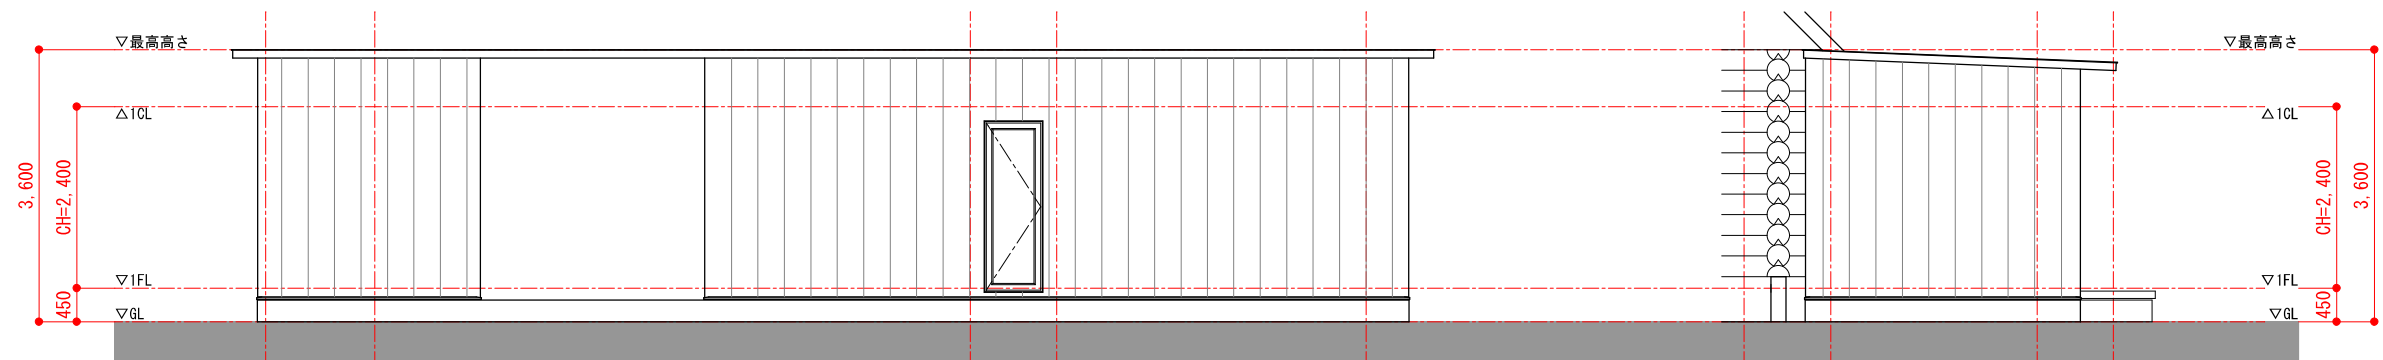

南側立面図 1 : 100

東側立面図 1 : 100

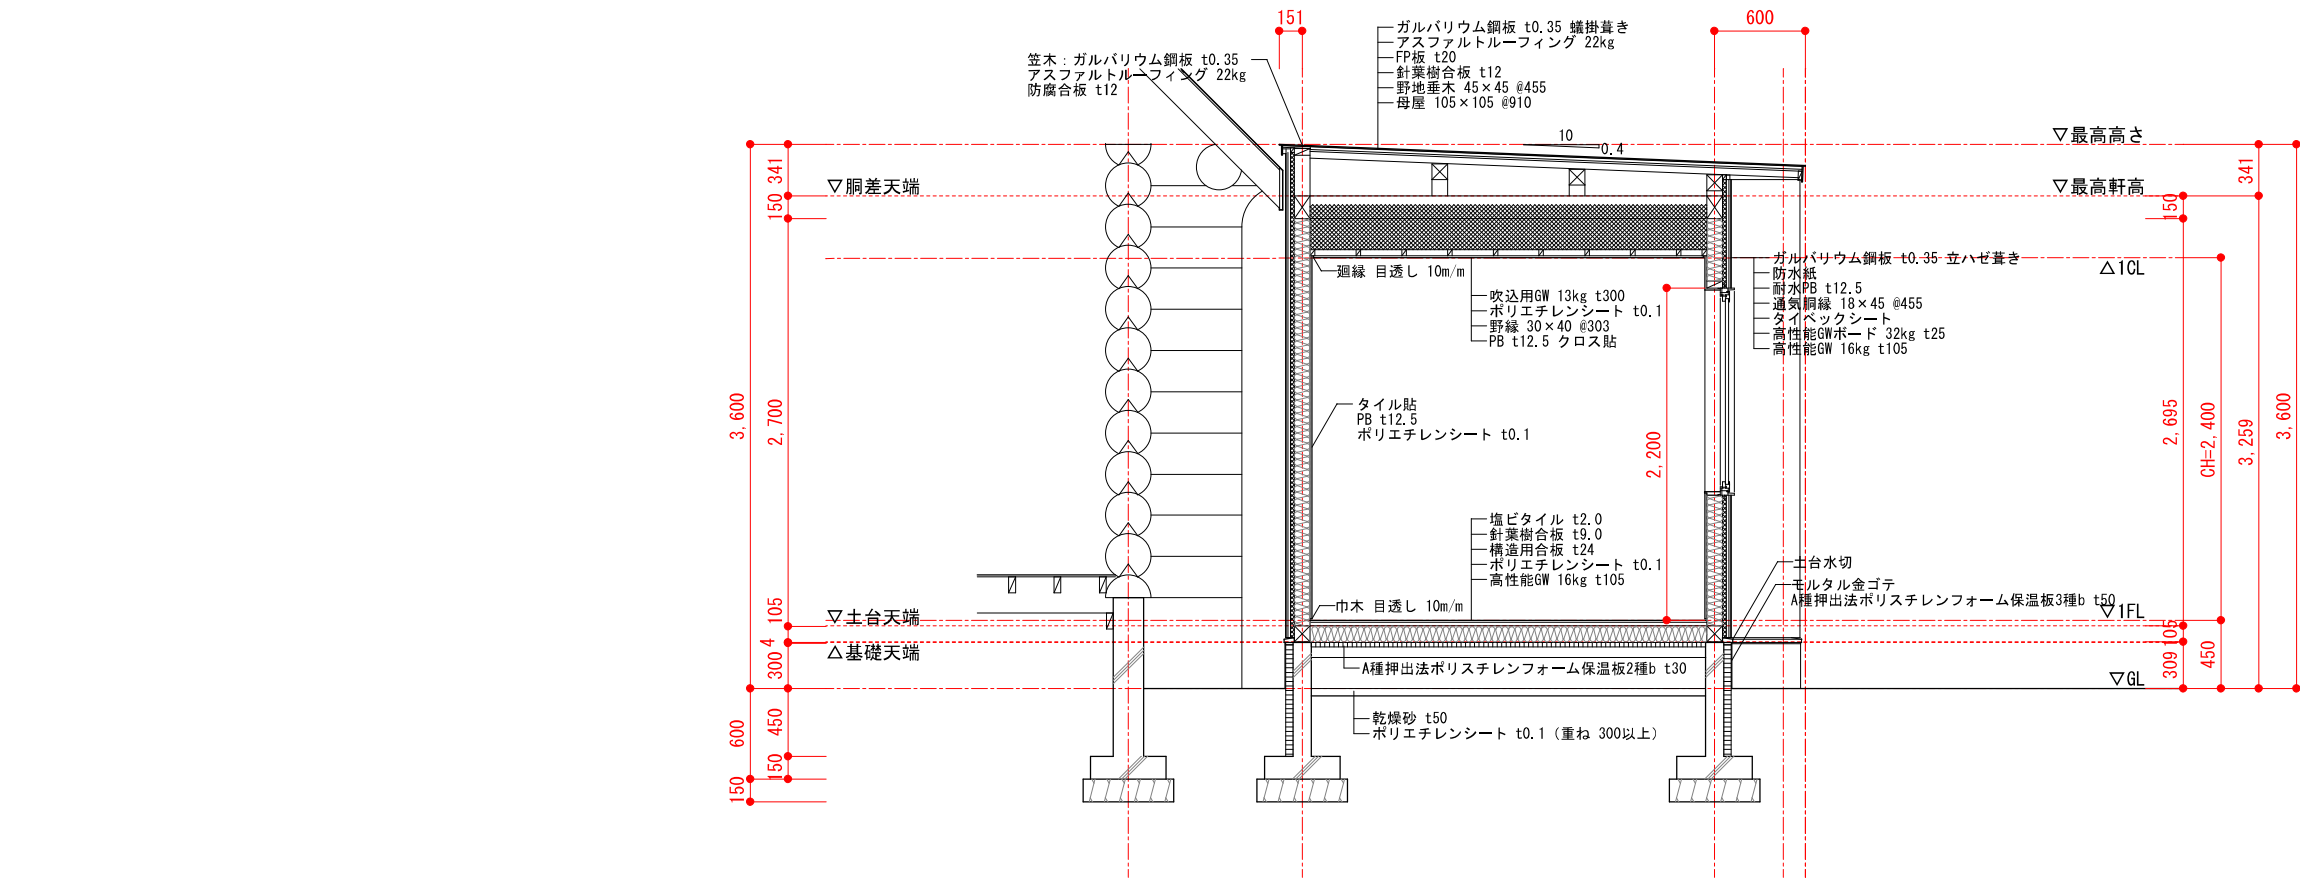

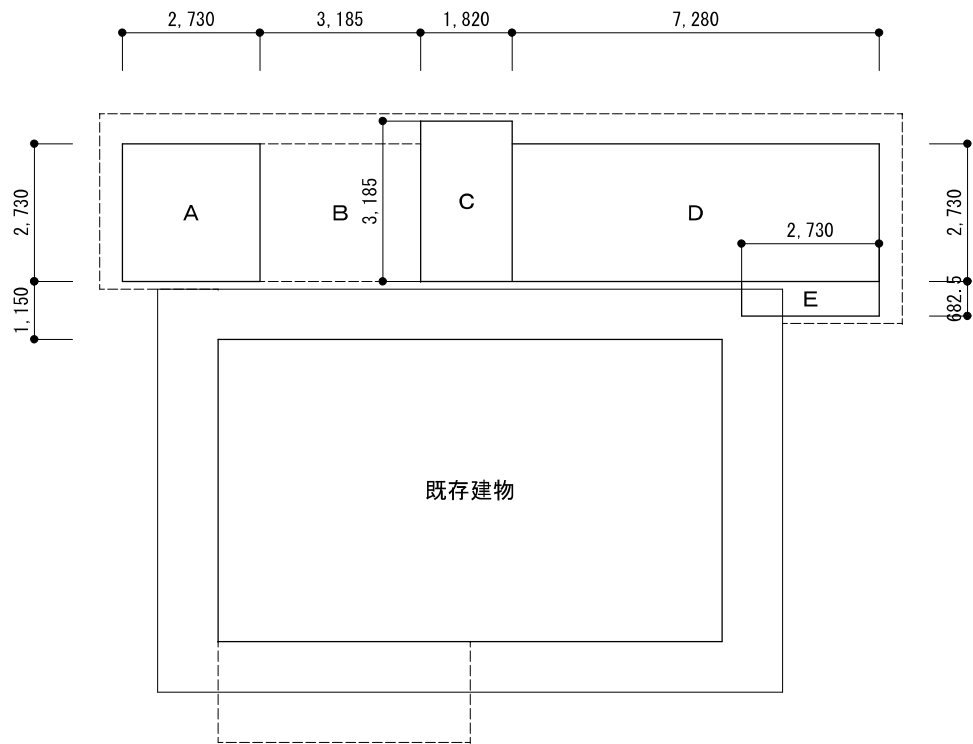



1 階求積図 1 : 150

申請建物求積図

	計 算 式		計
面積	A :	2.730 × 2.730	7.4529 m ²
	B :	3.185 × 2.730	8.69505 m ²
	C :	1.820 × 3.185	5.7967 m ²
	D :	7.280 × 2.730	19.8744 m ²
	E :	2.730 × 0.6825	1.863225 m ²
	階	計 算 式	合 計
延床面積	1 階	A + C + D + E 34.98723 m ²	34.99 m ²
容積算入 床 面 積	1 階	A + C + D + E 34.98723 m ²	34.99 m ²
建 築 面 積		A + B + C + D + E 43.68228 m ²	43.68 m ²

全体求積図

	計 算 式		計
延床面積	1 階	60.00 (既存建物) + 34.99 (申請建物) 94.99 m ²	140.99 m ²
	2 階	46.00 (既存建物)	
容積算入 床 面 積	1 階	60.00 (既存建物) + 34.99 (申請建物) 94.99 m ²	140.99 m ²
	2 階	46.00 (既存建物)	
建 築 面 積		70.00 (既存建物) + 43.68 (申請建物)	113.68 m ²

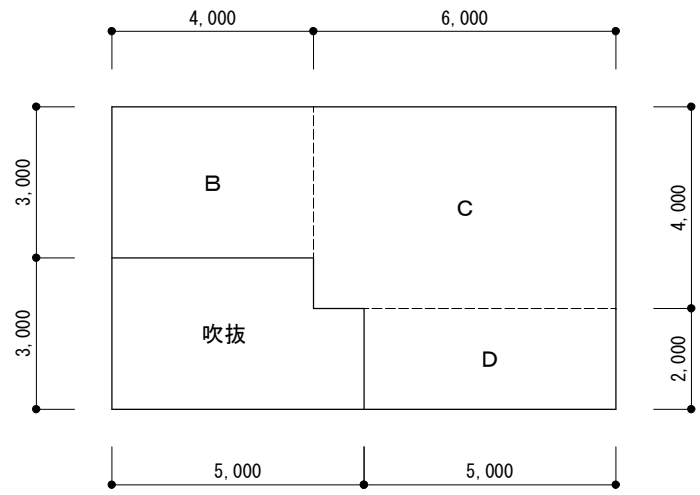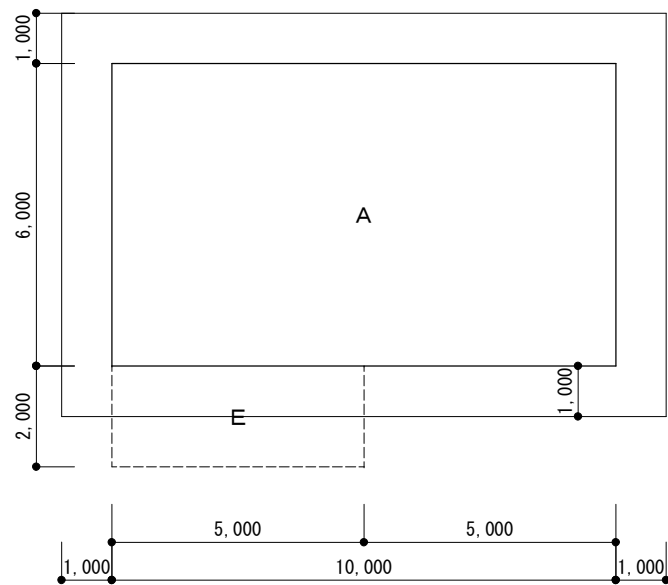

既存建物求積図

	計 算 式		計
面積	A : 10.000 × 6.000		60.00 m ²
	B : 4.000 × 3.000		12.00 m ²
	C : 6.000 × 4.000		24.00 m ²
	D : 5.000 × 2.000		10.00 m ²
	E : 5.000 × 2.000		10.00 m ²
	階	計 算 式	合 計
延床面積	1 階	A 60.00 m ²	106.00 m ²
	2 階	B + C + D 46.00 m ²	
容積算入 床 面 積	1 階	A 60.00 m ²	106.00 m ²
	2 階	B + C + D 46.00 m ²	
建 築 面 積		A + E 70.00 m ²	70.00 m ²

