


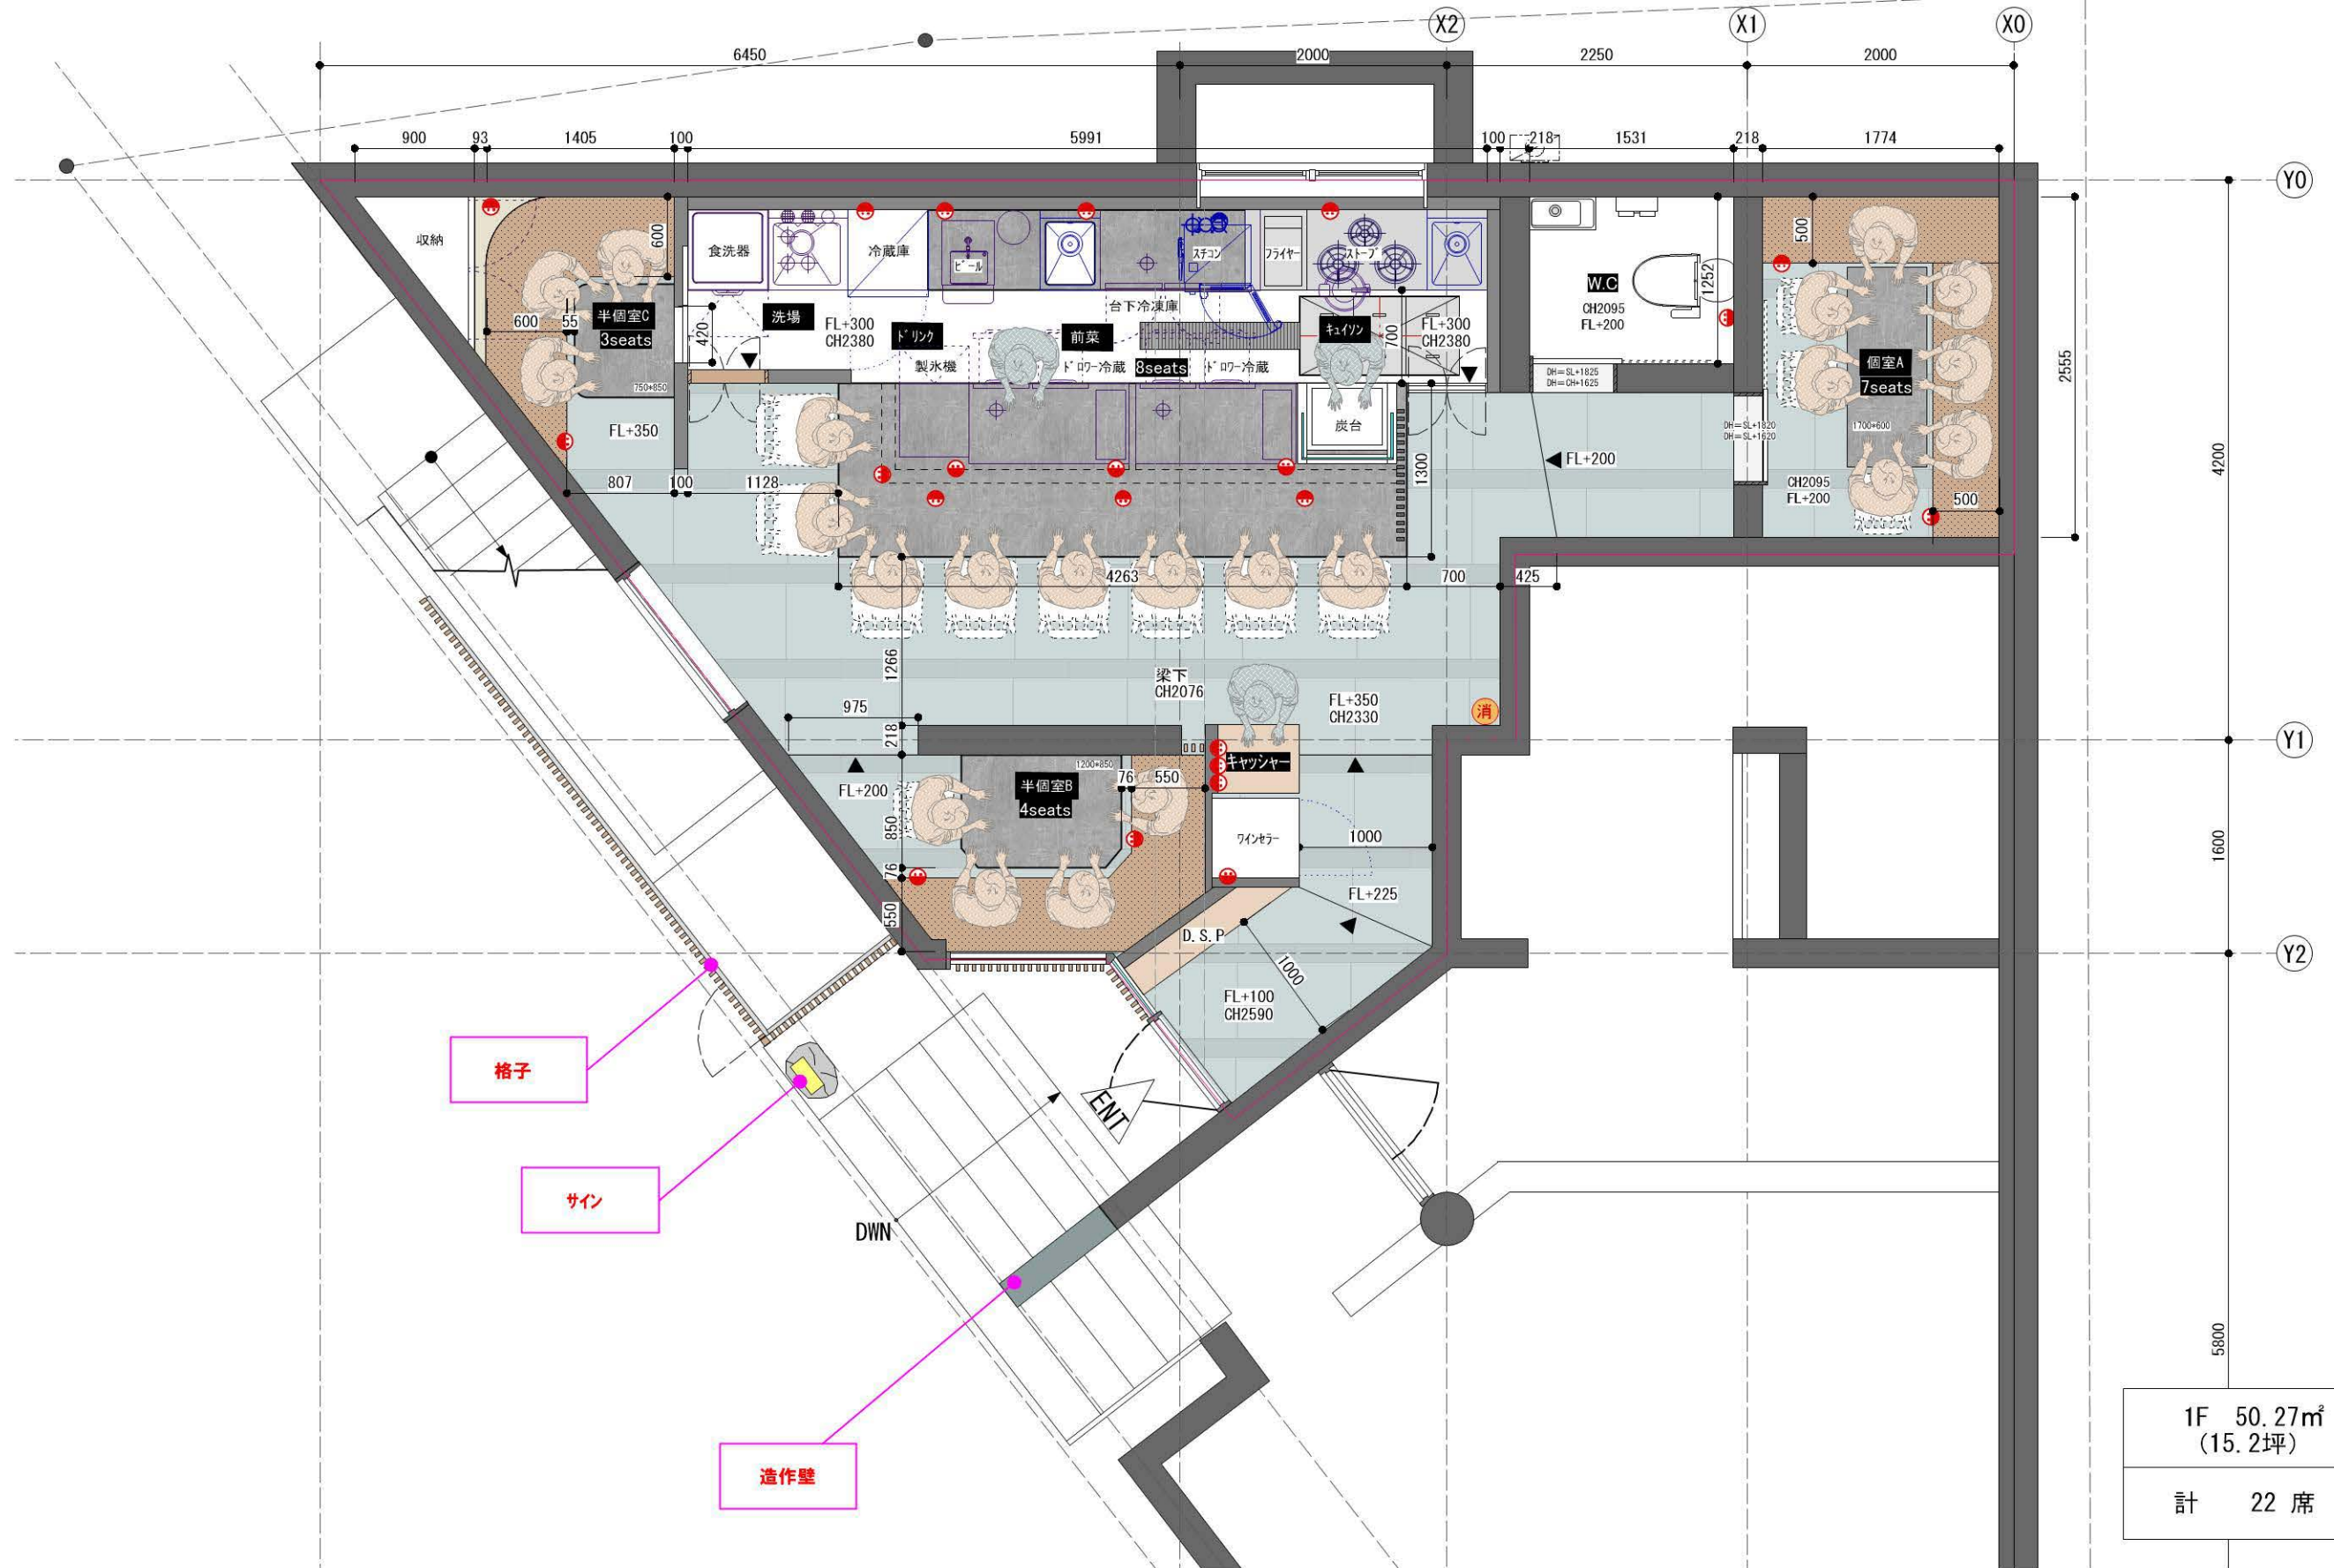

1F	50.27㎡ (15.2坪)
計	22 席

DATE	2026. 07. 26	N SQUARE interior design	PROJECT	乃木坂飲食店	SCALE	1/50 (A3)	TITLE	平面図	SEET NO.
									3

COUNTER IMAGE



ACCENT WALL

キッチン大理石風大判タイル



キッチンを象徴的に見せる
背景に迫力ある大判の石目調タイルを用います



吊棚には透け感の有る
アンバー色の大理石調パターンガラス

COUNTER TOP



アイランドカウンターは黒いモルタルを用います。

COUNTER CHAIR



アーム付きの落ち着いたカウンターチェア



FACADE IMAGE



縦格子



ACCENT WALL

キッチン大理石風大判タイル







乃木坂 和食店


打合せ図面

2026. 09. 21

〒107-0062 東京都港区南青山1-16-1 1F

N SQUARE
interior design

1	イメージパース
2	内装仕上表
3	平面図
4	厨房図
5	天井伏図
6	照明計画図
7	照明器具表
8	展開位置指示図
9	外観図
10	展開図-1
11	展開図-2
12	展開図-3
13	展開図-4
14	給排気図
15	給排水・ガス設備図
16	ファニチャー計画
17	電気設備図
18	
19	
20	
21	
22	

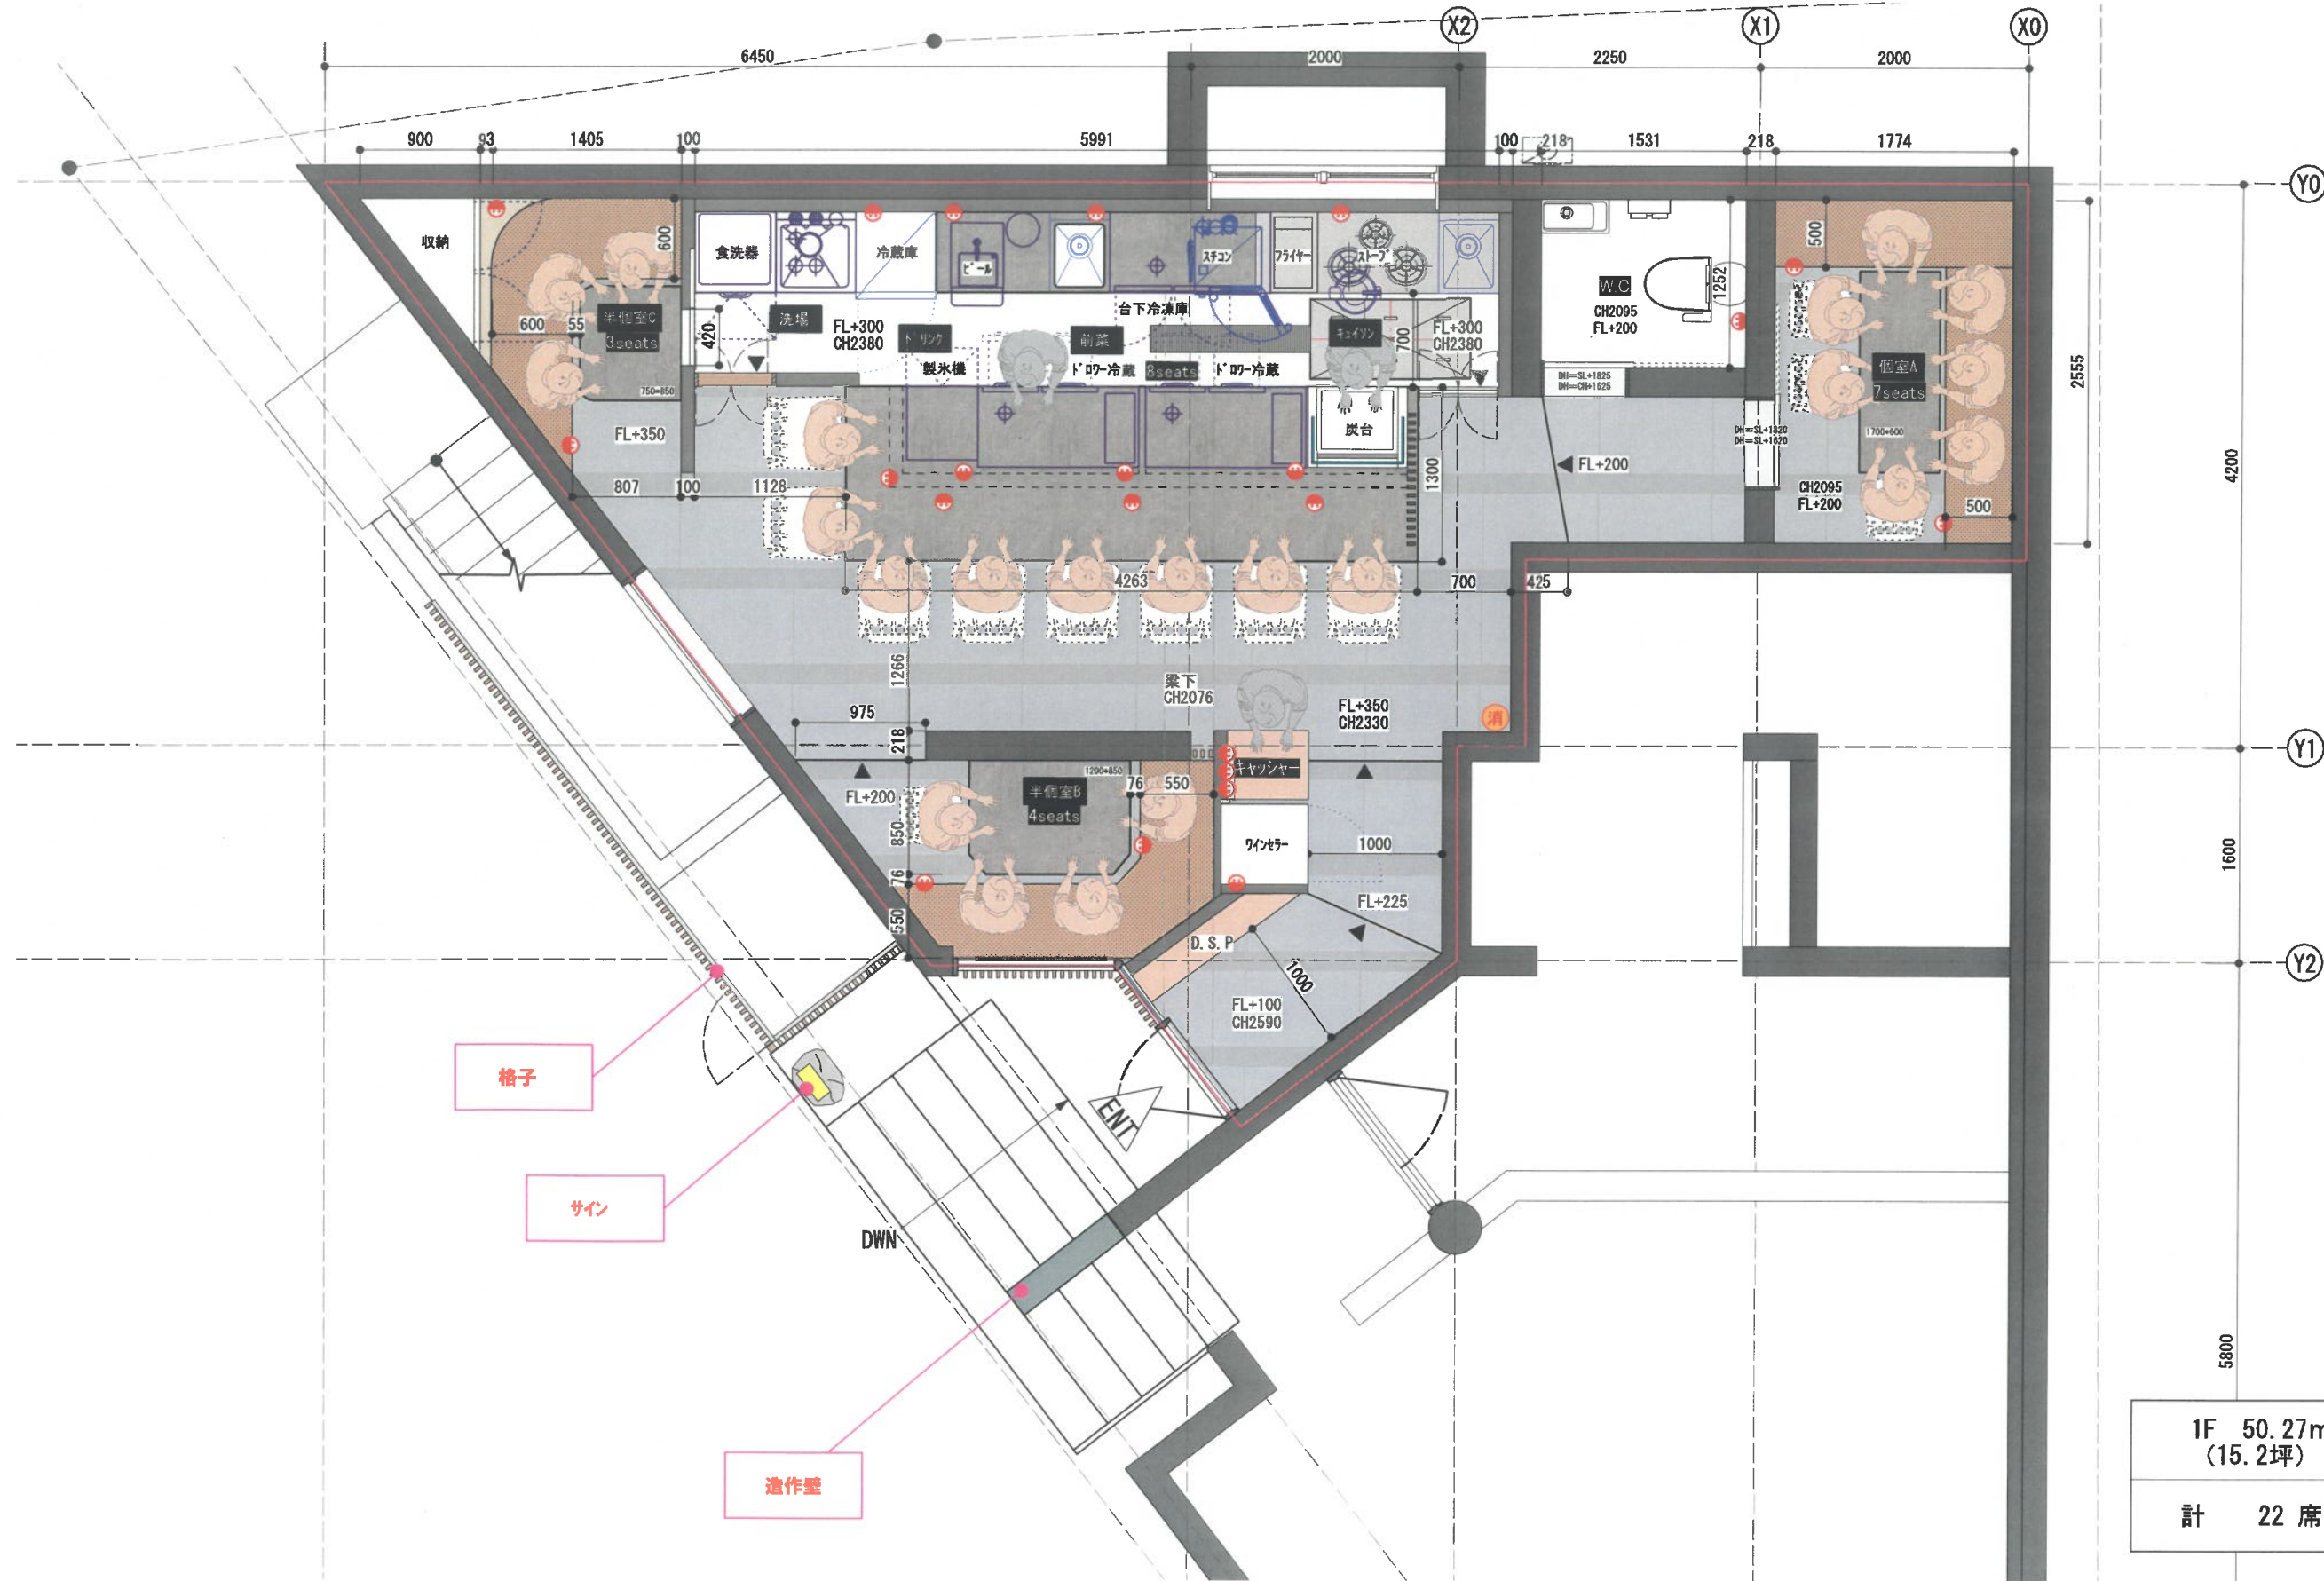

1F	50.27㎡ (15.2坪)
計	22 席

DATE	2026. 07. 26	N SQUARE interior design	PROJECT	乃木坂飲食店	SCALE	1/50 (A3)	TITLE	平面図	SEET NO.
									3

仕上表

室名	床	巾木	腰壁	壁	天井	備考
ファサード	既存	既存	既存	格子造作	既存	サイン設置
客席	フリーフロア軸バネティクル+コンパネ 下地調整の上 タイル貼り CCN-60-247ントラチ [株式会社サンワ]	スチールクロカワ 60mm t=1mm	躯体コンクリート 一部PB12. 5m/m下地 モルタル金鍍	躯体コンクリート 一部PB12. 5m/m下地 墨モルタル金鍍	スkeleton天井 一部EP塗装	
カウンター	フリーフロア軸バネティクル+コンパネ 下地調整の上 タイル貼り CCN-60-247ントラチ [株式会社サンワ]	PB12. 5m/m下地 ペニアビーリング 貼りOS. CL	PB12. 5m/m下地 ペニアビーリング 貼りOS. CL	PB12. 5m/m 墨モルタル金鍍	ケイカル5m/m下地 グレーエージング 塗装	天板:モールドテックス ブラック つや消しトップコート
キッチン	均しモルタルの上シート防水 保護モルタル スタイロ敷き シンター打設 モルタル金ゴテ仕上	モルタル金鍍h200	ケイカル9m/m下地 濃いグレー塗装	ケイカル9m/m下地 タイル貼りBLU JE6 12RM[ダイワワン]	ケイカル5m/m下地 グレーエージング 塗装	棚造作
トイレ	フリーフロア軸バネティクル+コンパネ 下地調整の上 タイル貼り CCN-60-247ントラチ [株式会社サンワ]	スチールクロカワ 60mm t=1mm	躯体コンクリート	躯体コンクリート	既存PB12. 5m/m下地 EP艶消し白塗装	吊棚造作 一部ミラー貼り
個室	フリーフロア軸バネティクル+コンパネ 下地調整の上 タイル貼り CCN-60-247ントラチ [株式会社サンワ]	スチールクロカワ 60mm t=1mm	躯体コンクリート PB12. 5m/m下地 不燃ビーリング 材貼	躯体コンクリート PB12. 5m/m下地 不燃ビーリング 材貼	スkeleton天井	



セメント調タイル貼
597*597*9. 8
CCN-60-247ントラチ
[株式会社サンワ]



厨房・カウンター 石目タイル
BLU JE6 12RM[ダイワワン]
597*1196*6. 5



カウンターボデー照明ガラス
アンバー型板硝子 ガラスランド

DATE
2026. 09. 20

PROJECT


SCALE

TITLE
仕上表

乃木坂 和食店

N SQUARE
interior design

SEET NO.
02

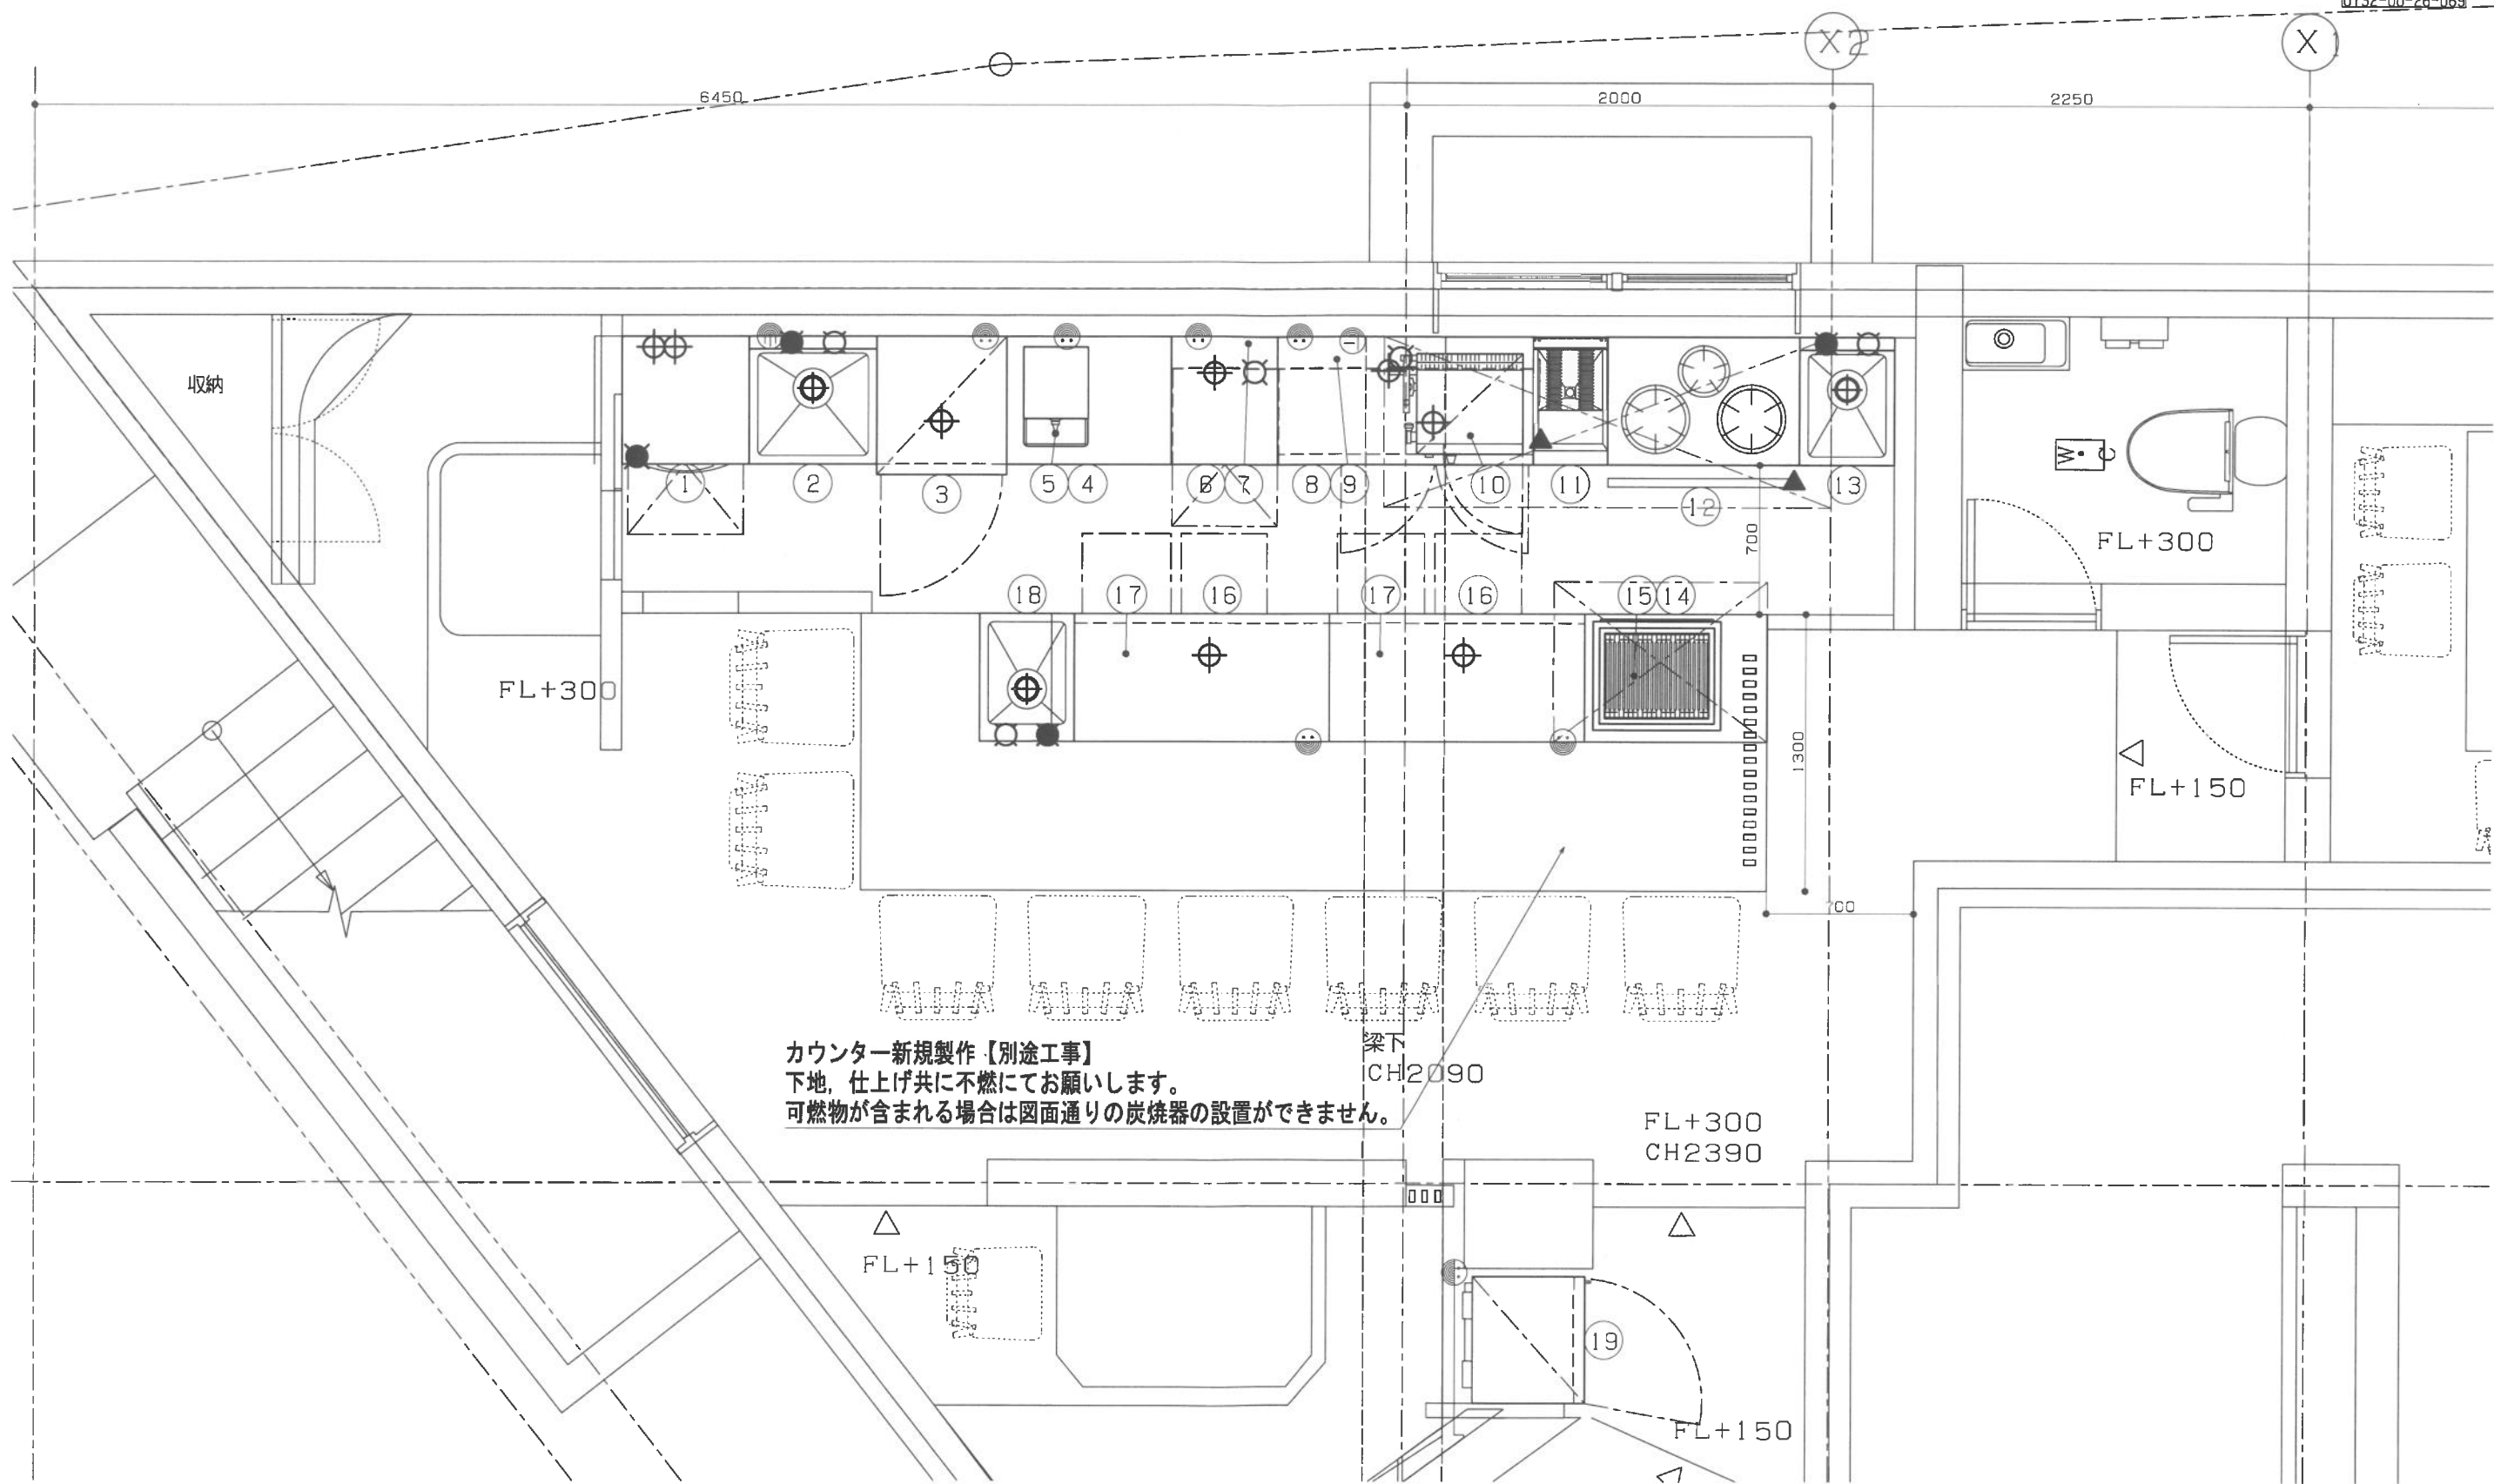

⚠ 当厨房設計図書は、厨房室の下地材及び仕上材は、不燃材料と見なしてあります。

注記 別途工事：給水・給湯・排水・蒸気・ガス・電気等の一次配工事・二次配配線工事、給湯器、水栓、鍋架、グリストラップ、排気フード、手洗器、吊ボルト工事、壁下地補強
本図面上でトラップ付属の厨房機器はシンク型・冷蔵庫のみとなります。排水温度が100℃になる可能性がある機器製品には「高温」、80℃以下の機器製品には「新機種」と表記してあります。

特記 *


建築設備記号		設備シンボル凡例	
準備/火機連に準拠しているか		給水	ガス
建物	厨房部分	給湯	ガスホース
		排水	冷却水
		床排水	蒸気

設備シンボル凡例	
1φ100V	排気フード
1φ200V	換気扇
3φ200V	天井機 (H5)

tanico


設計	縮尺	現場名	図番
巻口	1/50 (A3)	乃木坂和食飲食店	1
製図	営業	名称	最終更新日
巻口	佐藤	厨房配置平面図	2026/09/17

	天井エアコン
	壁掛けエアコン
	非常照明 既存
	避難誘導灯 既存
	天井換気扇 既存
	HS 給気吹出口 既存
	消火器
	BGM スピーカー 内装工事にて設置 アンプ、スピーカー内装工事

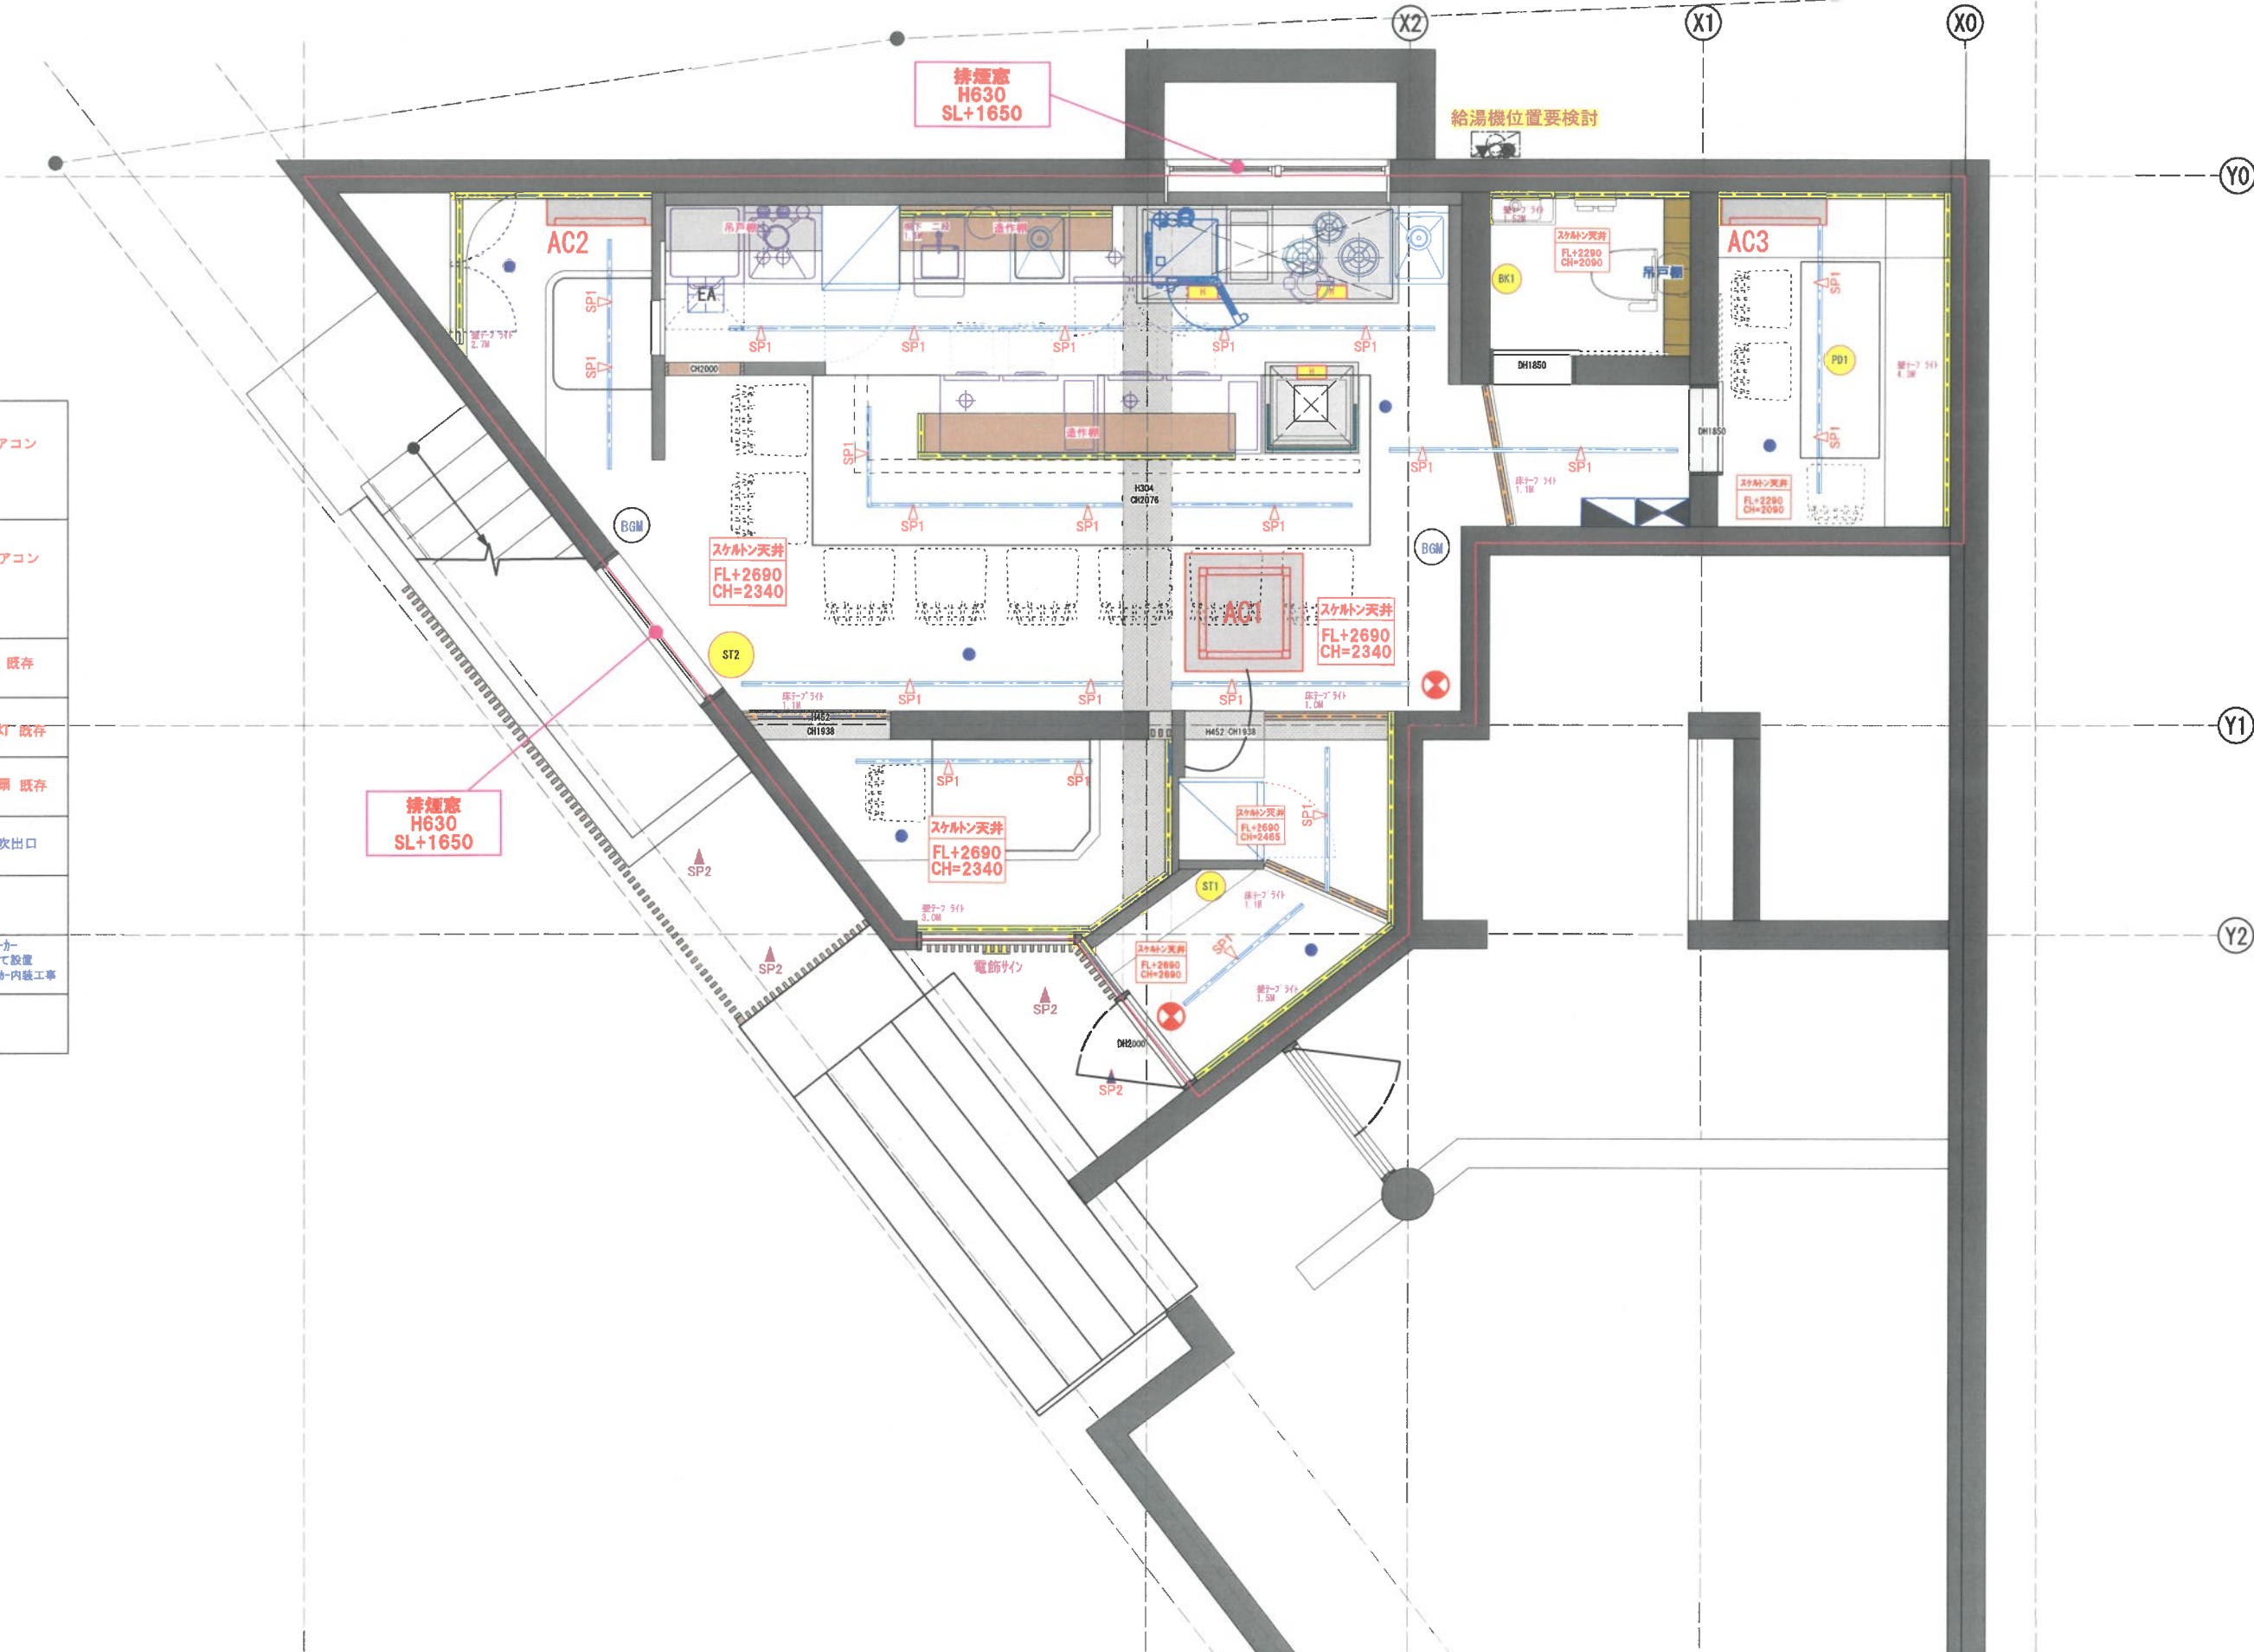


DATE	2026. 09. 09	PROJECT	乃木坂飲食店	SCALE	1/50 (A3)	TITLE	天井伏図	SEET NO.
								05

N SQUARE
interior design

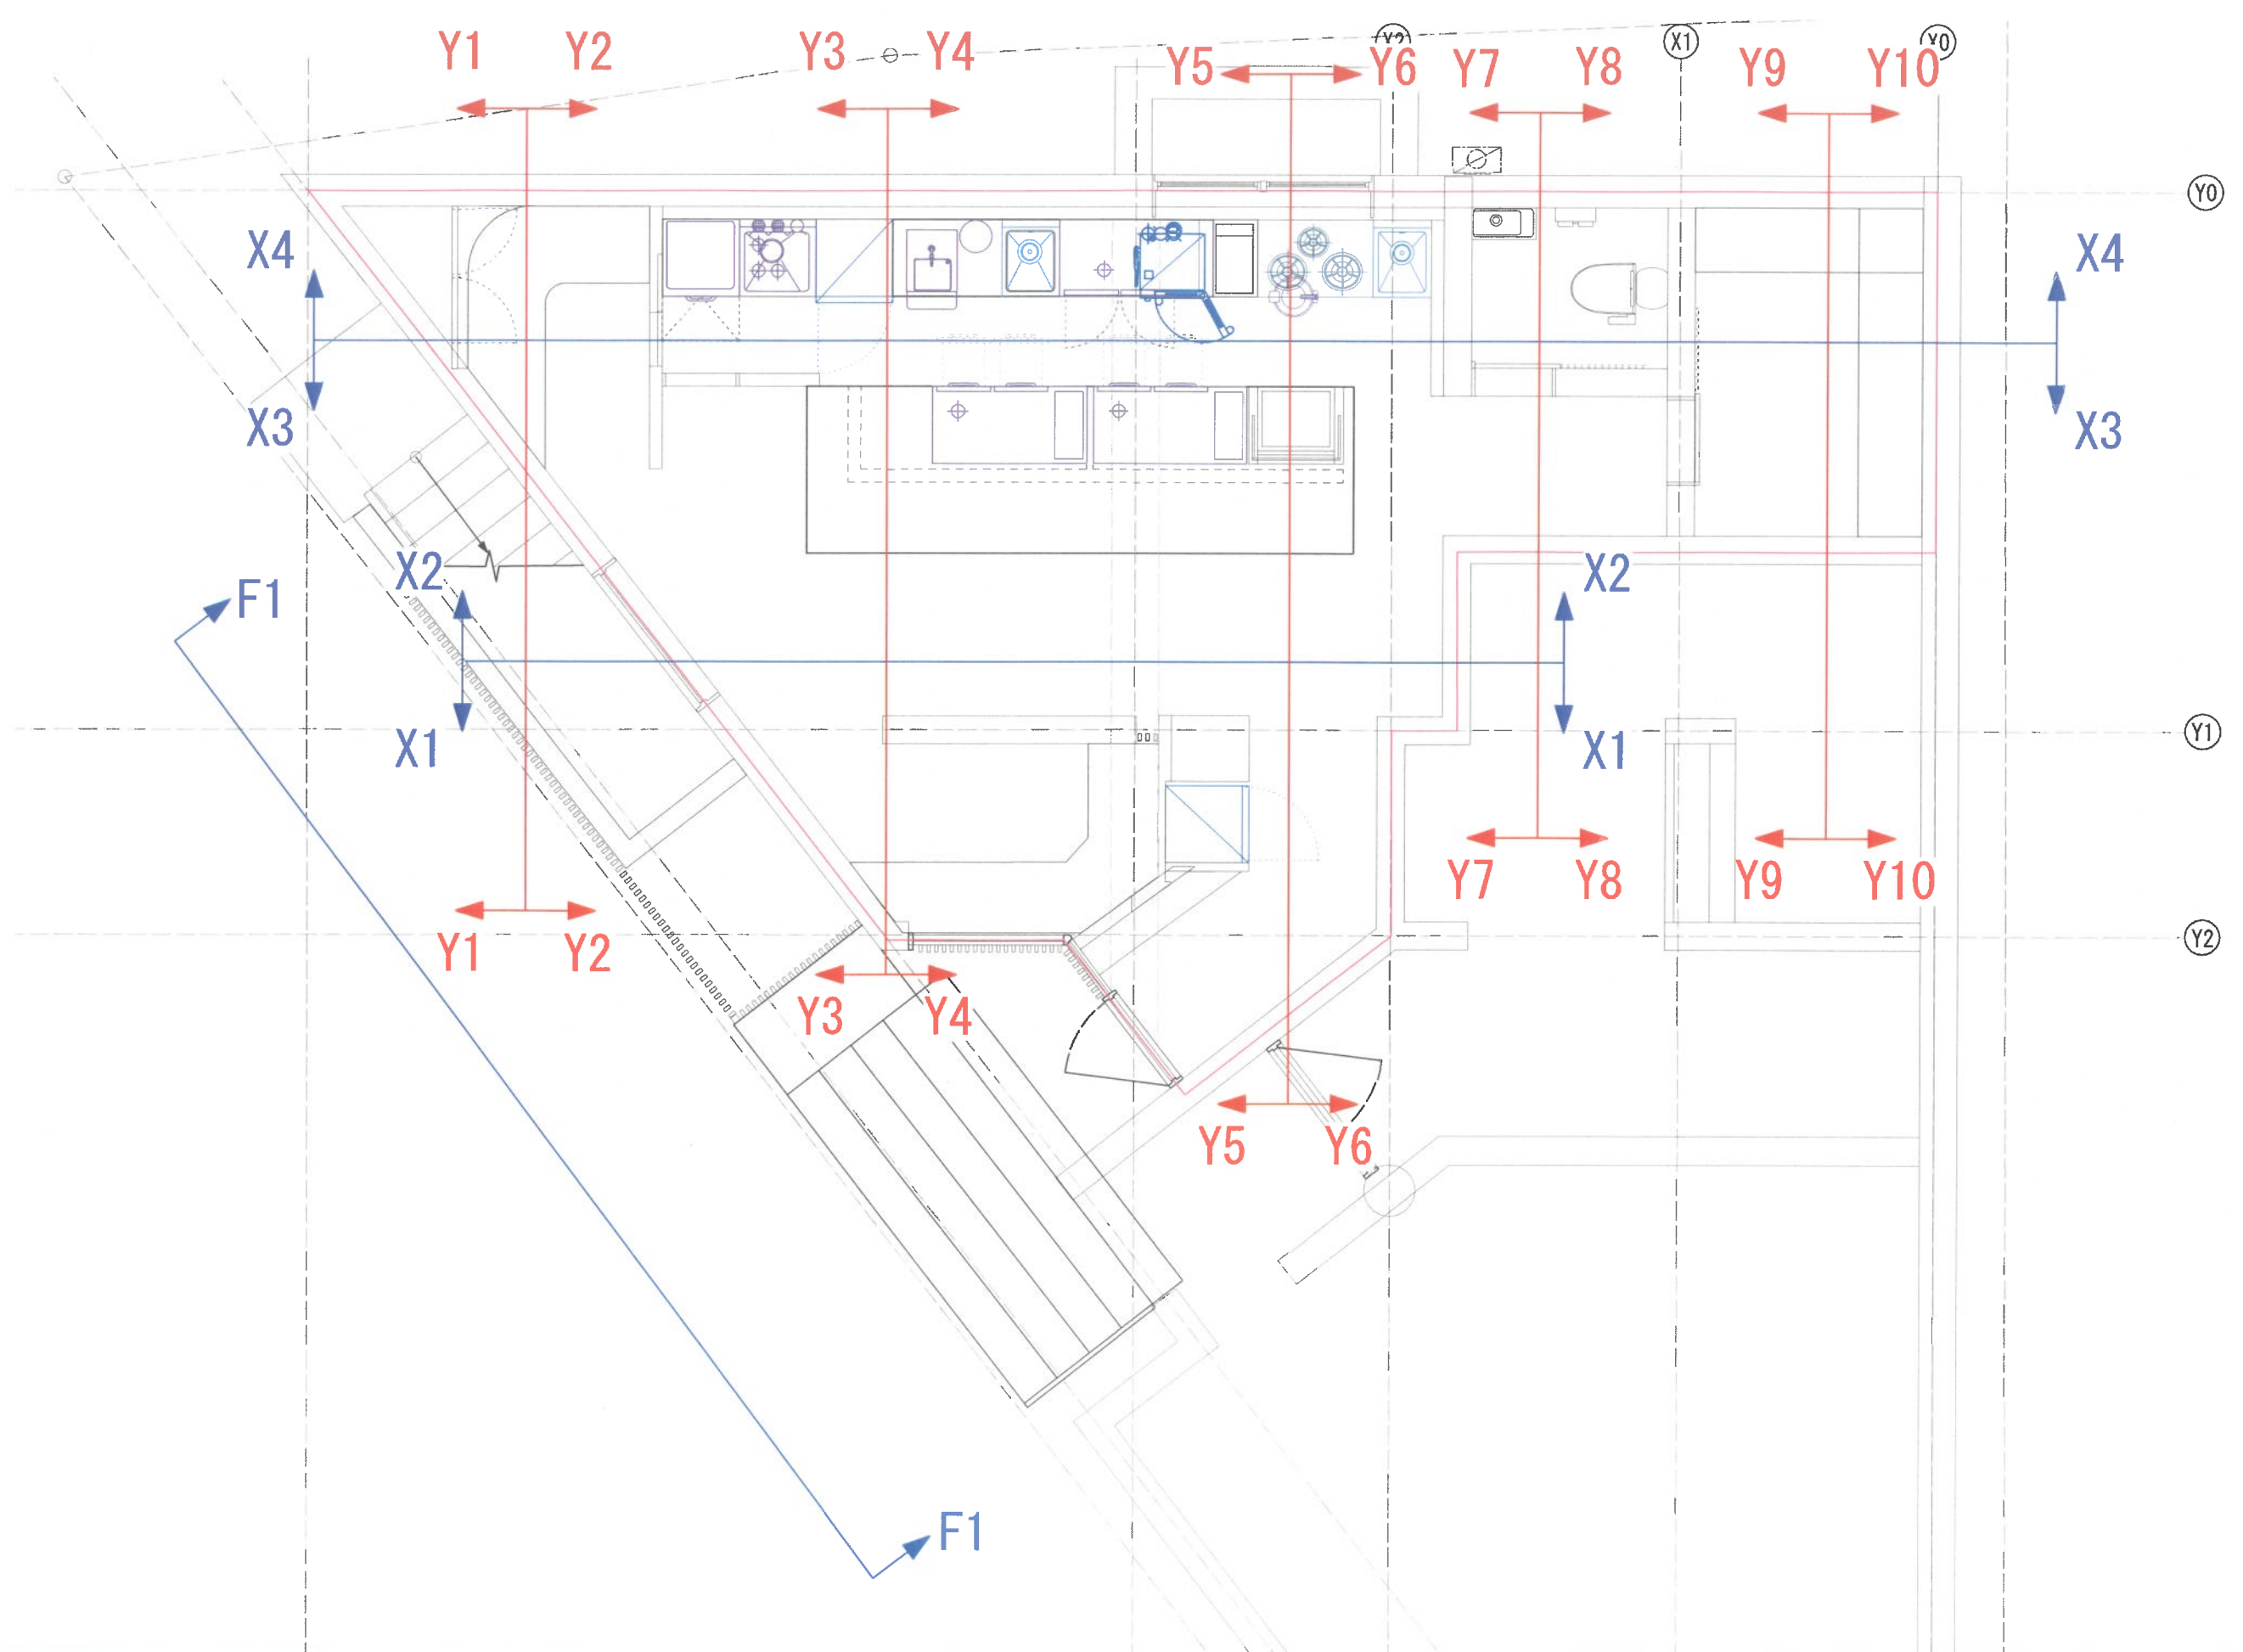

DATE	2026. 09. 09	N SQUARE interior design	PROJECT	乃木板飲食店	SCALE	1/50 (A3)	TITLE	展開断面位置	SEET NO.
									8

F1

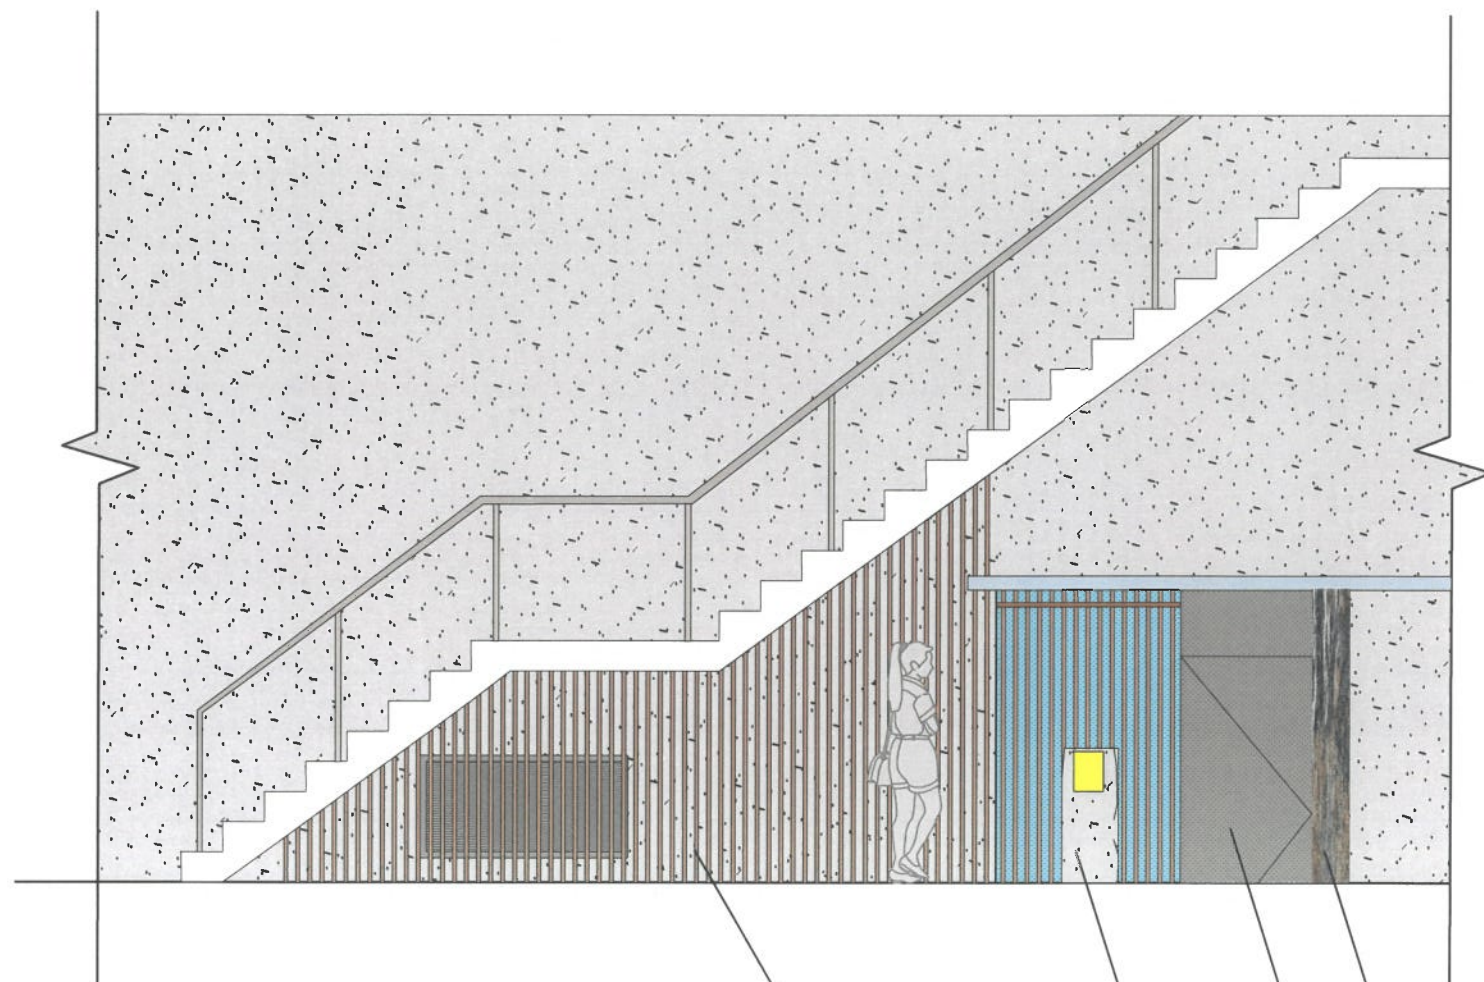


格子設置
サイディング材
ブラック木目
一部メンテナンス扉

石堀込
上部サイン

袖壁
大判タイル貼り

既存鉄扉黒717塗装

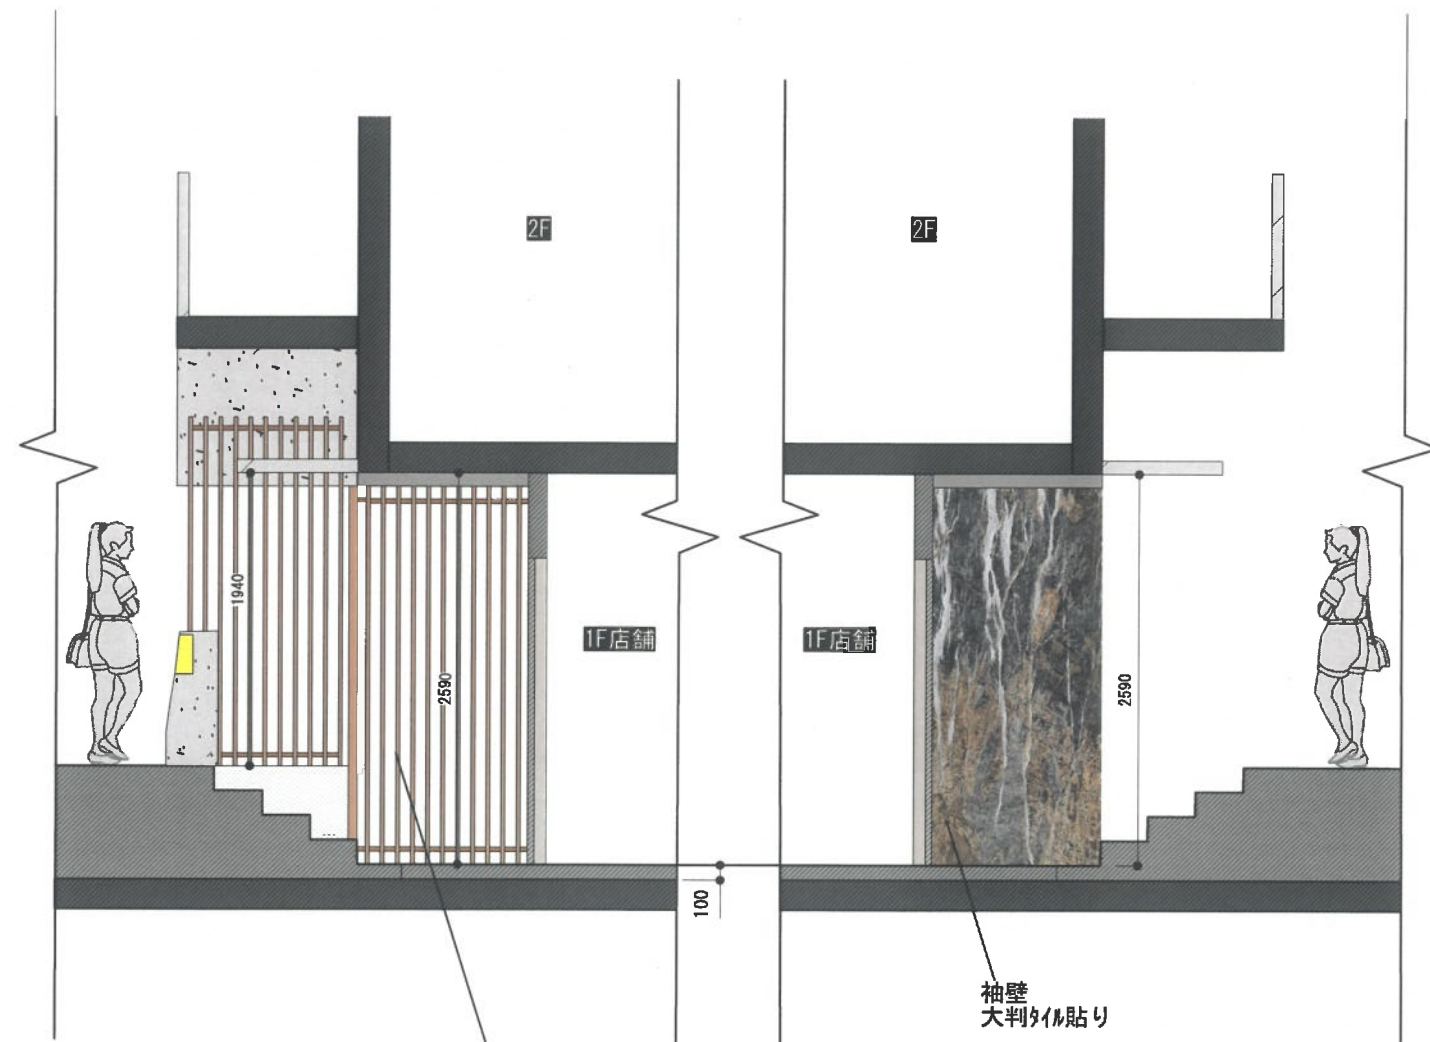


格子設置
サイディング材
ブラック木目
一部メンテナンス扉


袖壁
大判タイル貼り

DATE	2026.09.19	PROJECT 乃木坂 和食店	SCALE 1/50 (A3)	TITLE 外観図	SEET NO. 9

N SQUARE
interior design

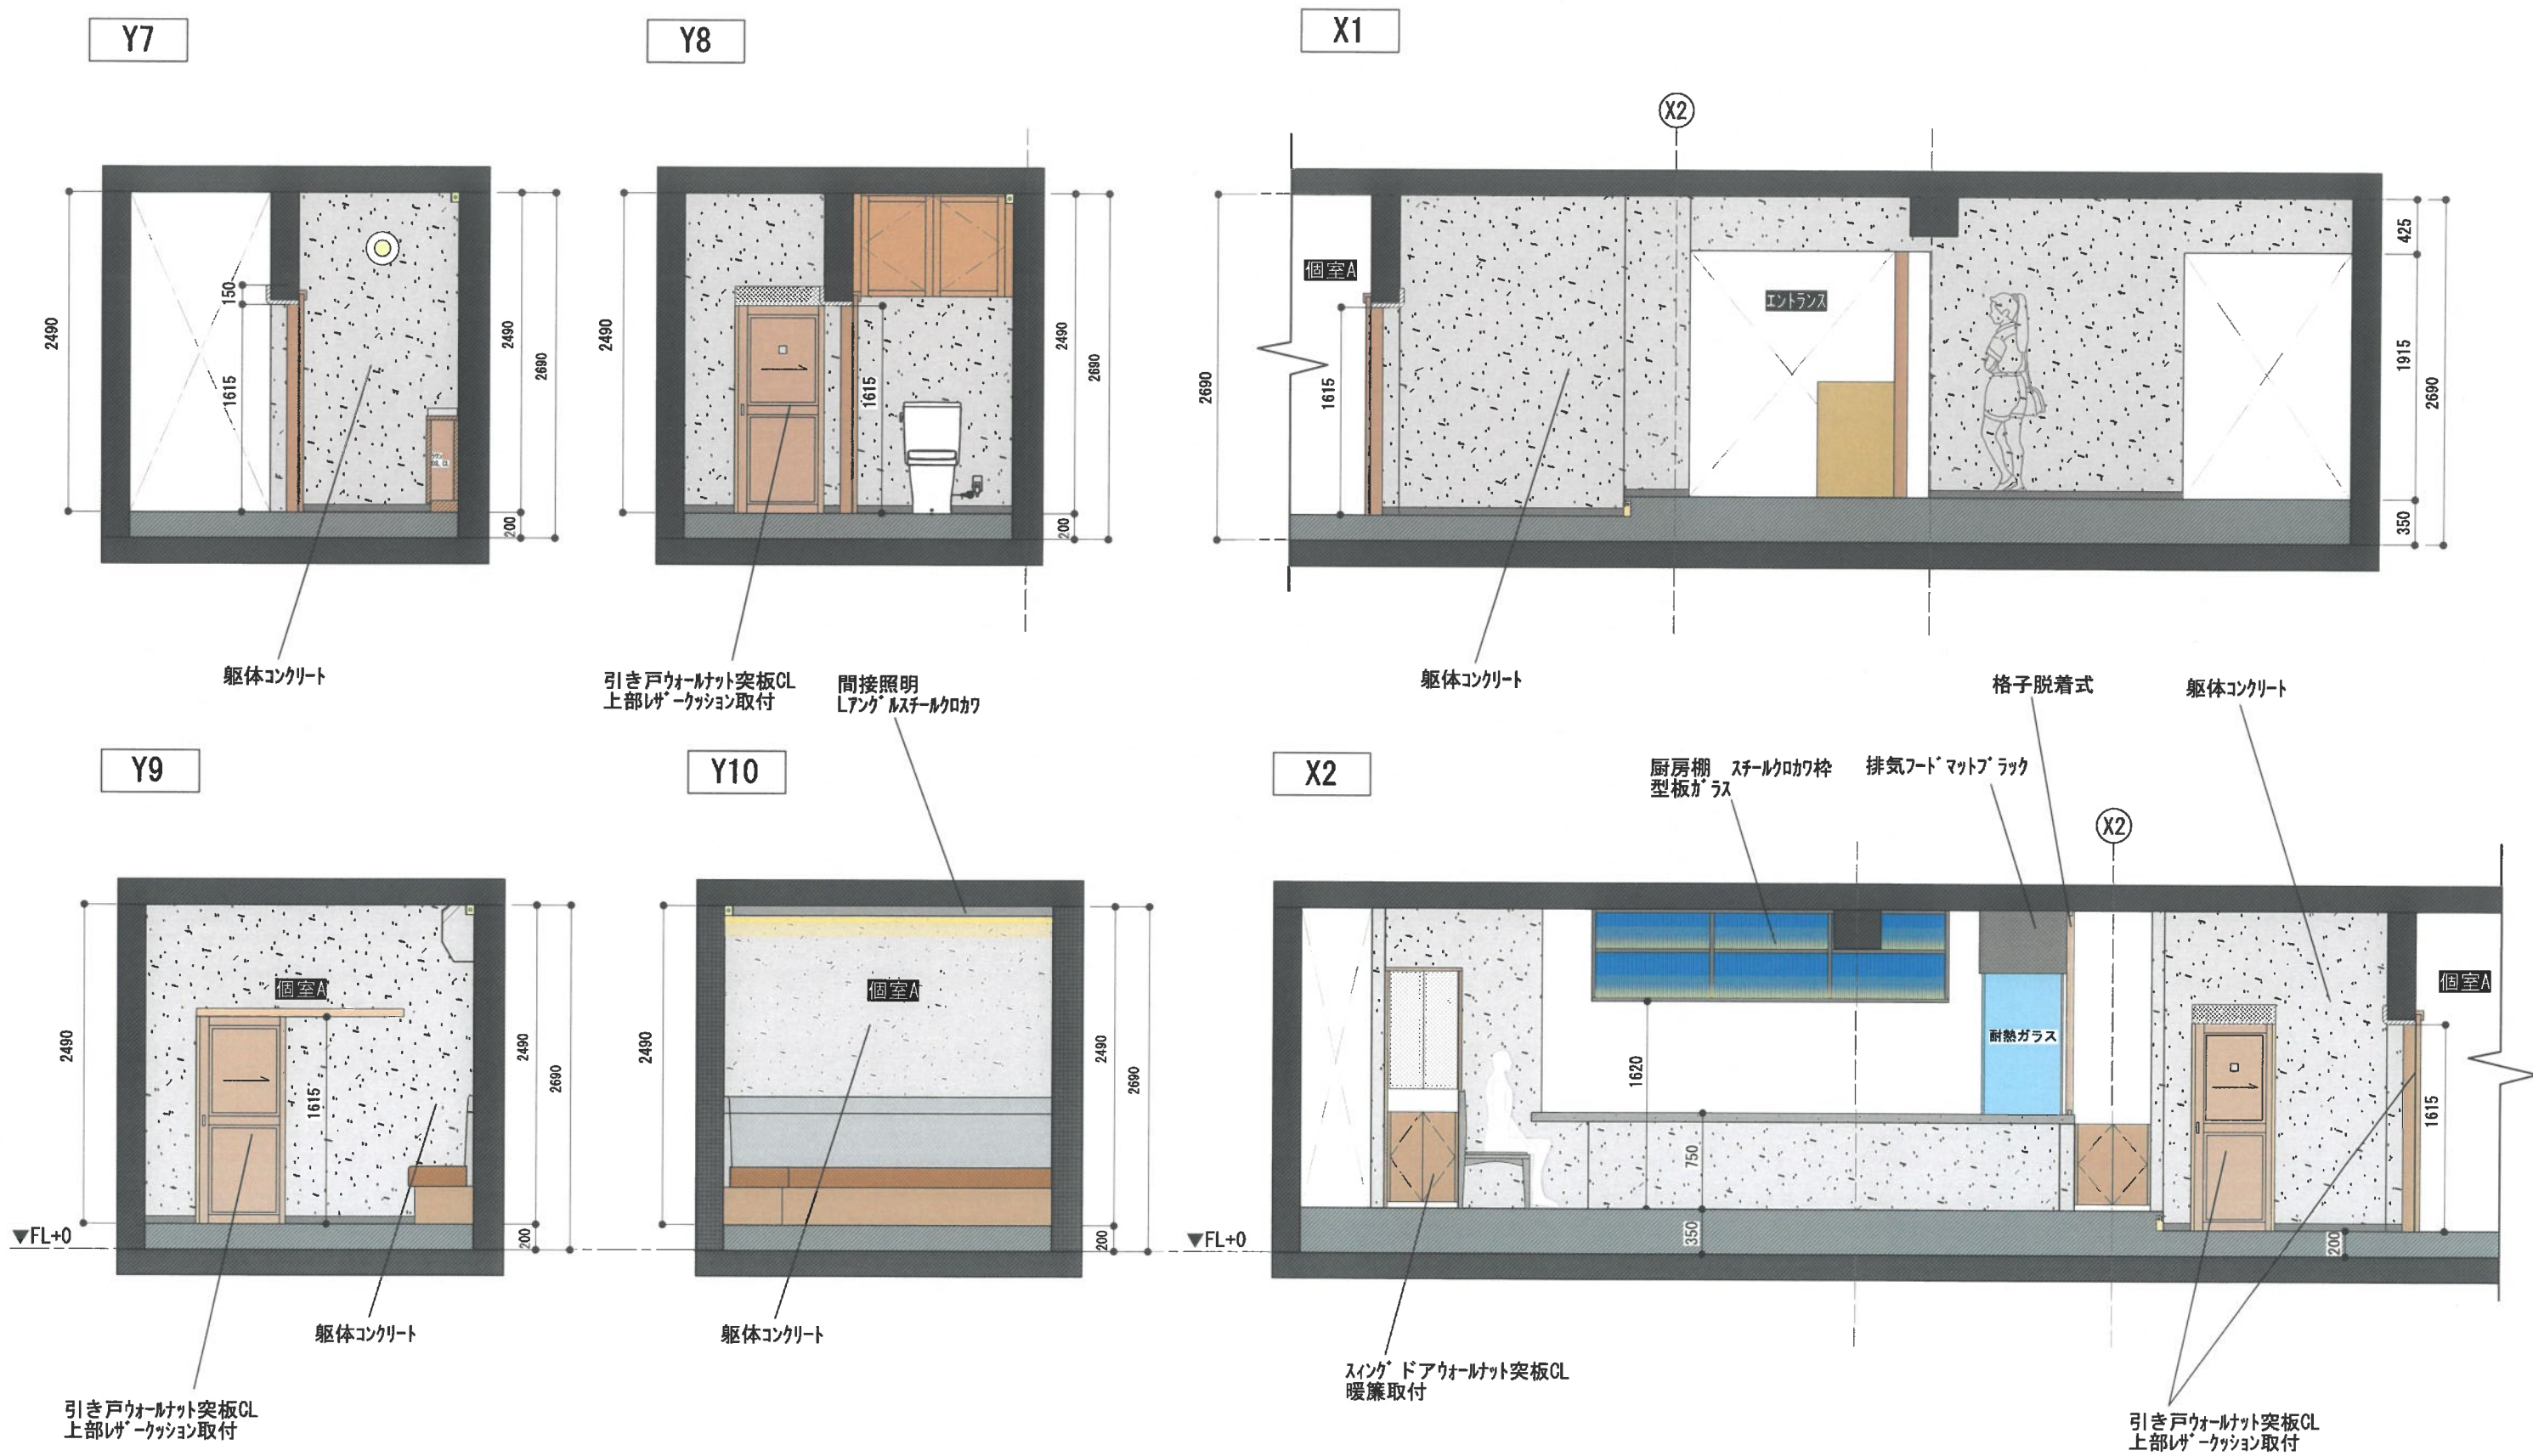


DATE	2026.09.19	N SQUARE interior design	PROJECT	乃木坂 和食店	SCALE	1/50 (A3)	TITLE	展開図-2	SEET NO.
									11

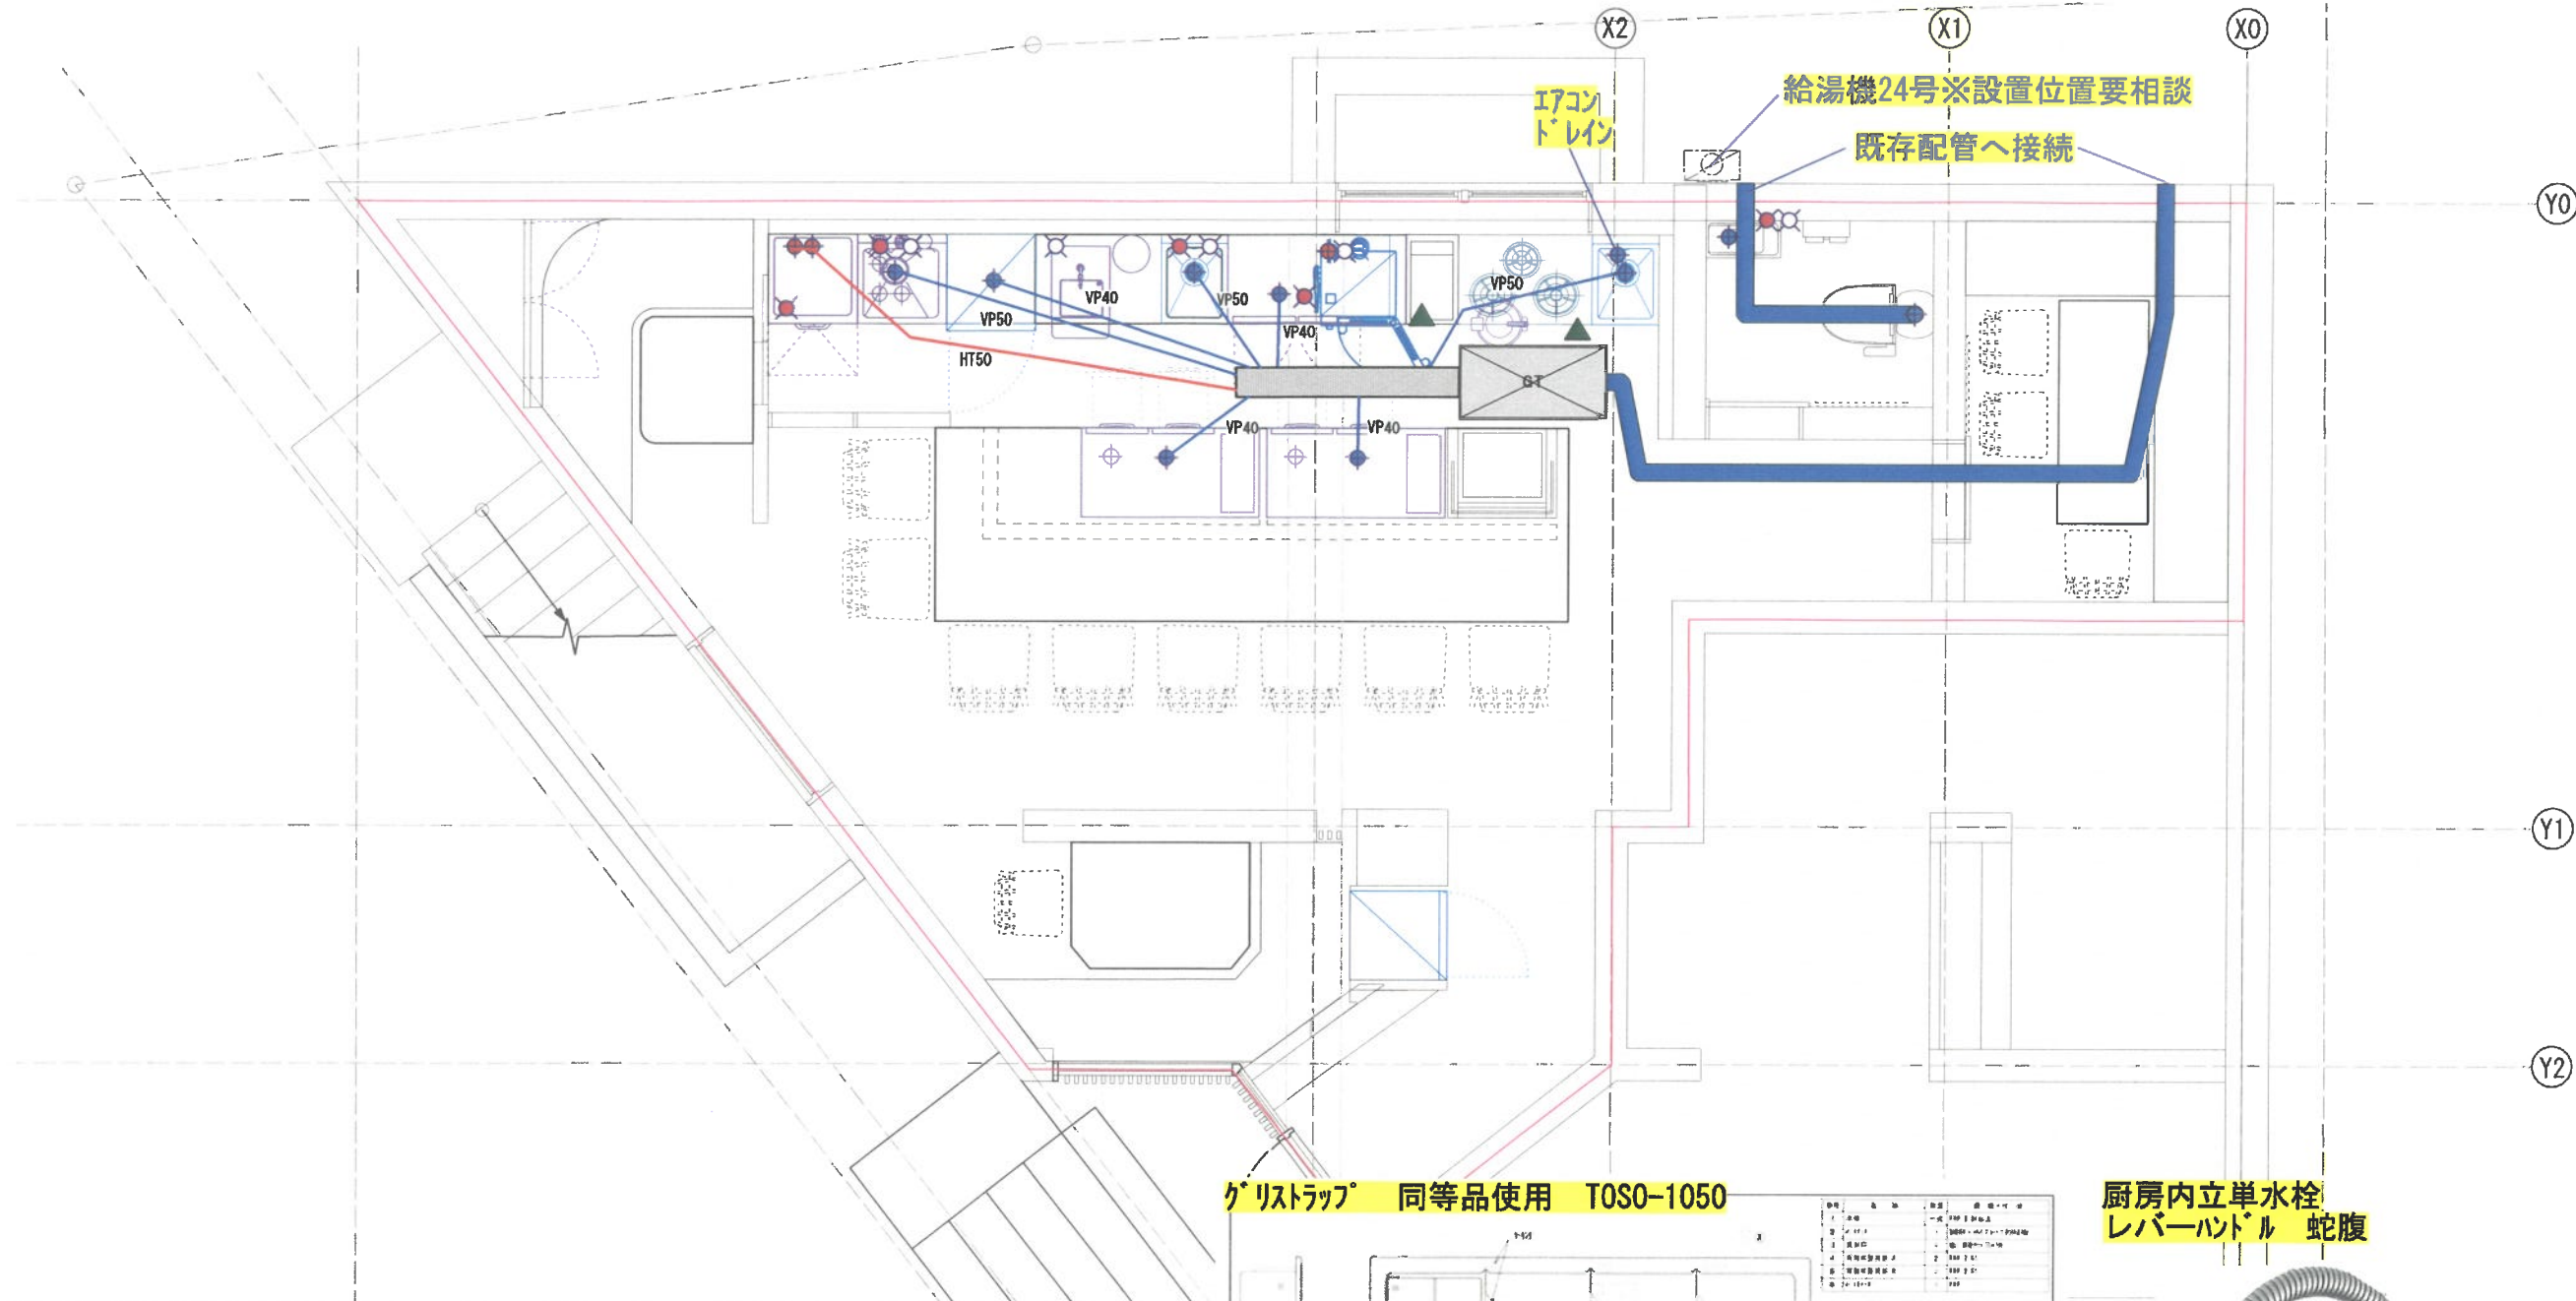


ゲリストラップ 同等品使用 TOSO-1050

厨房内立単水栓
レバーハンドル 蛇腹

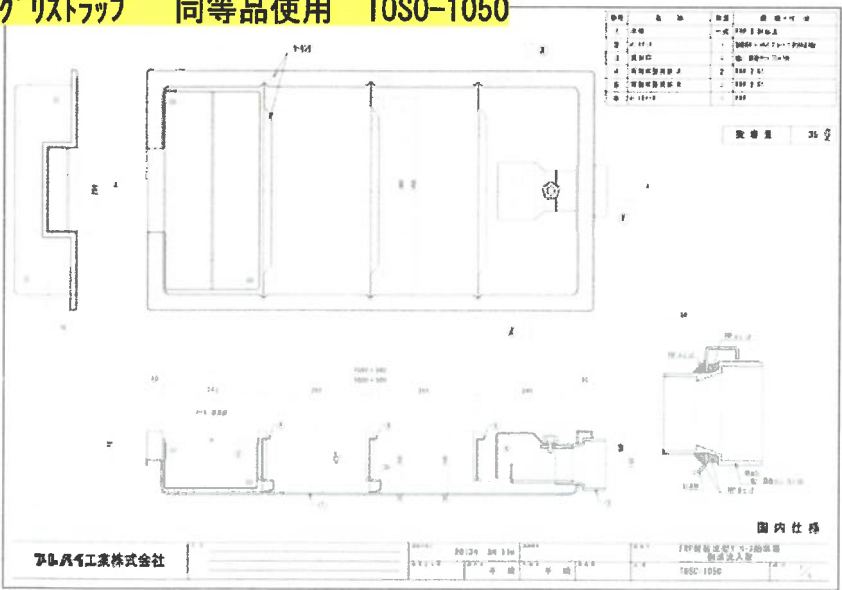

- 【注記】
1. 厨房内排水管はシンダー内配管。
 2. 配管の器具接続位置・配管接続サイズ・排水立ち上げ位置は厨房機器設備位置図を参照し、機器納品業者と十分打合せの上決定すること。
 3. 給水・給湯・ガス管への接続にはバルブを設置すること。
 4. 配管接続の際に異種金属を用いる場合は、絶縁継ぎ手を使用すること。
 5. 給水・給湯管には逆止弁を使用すること。
 6. 天井内等隠蔽部の給水・給湯管には保温防露を施すこと。
 7. ガス設備のガスメーター・配管サイズは、ガス供給会社との協議の上決定すること。
 8. 配管ルート等は、現場状況により適宜調整すること。
 9. 区画貫通部の貫通処理は、大臣認定工法以上とすること。また、施工記録を漏れなく残すこと。
 10. 厨房内で熱の影響がある部分は、断熱施工とすること。もしくは塩ビ管の使用を避けること。
 11. 設計指針書記載の指定配管材料を使用すること。

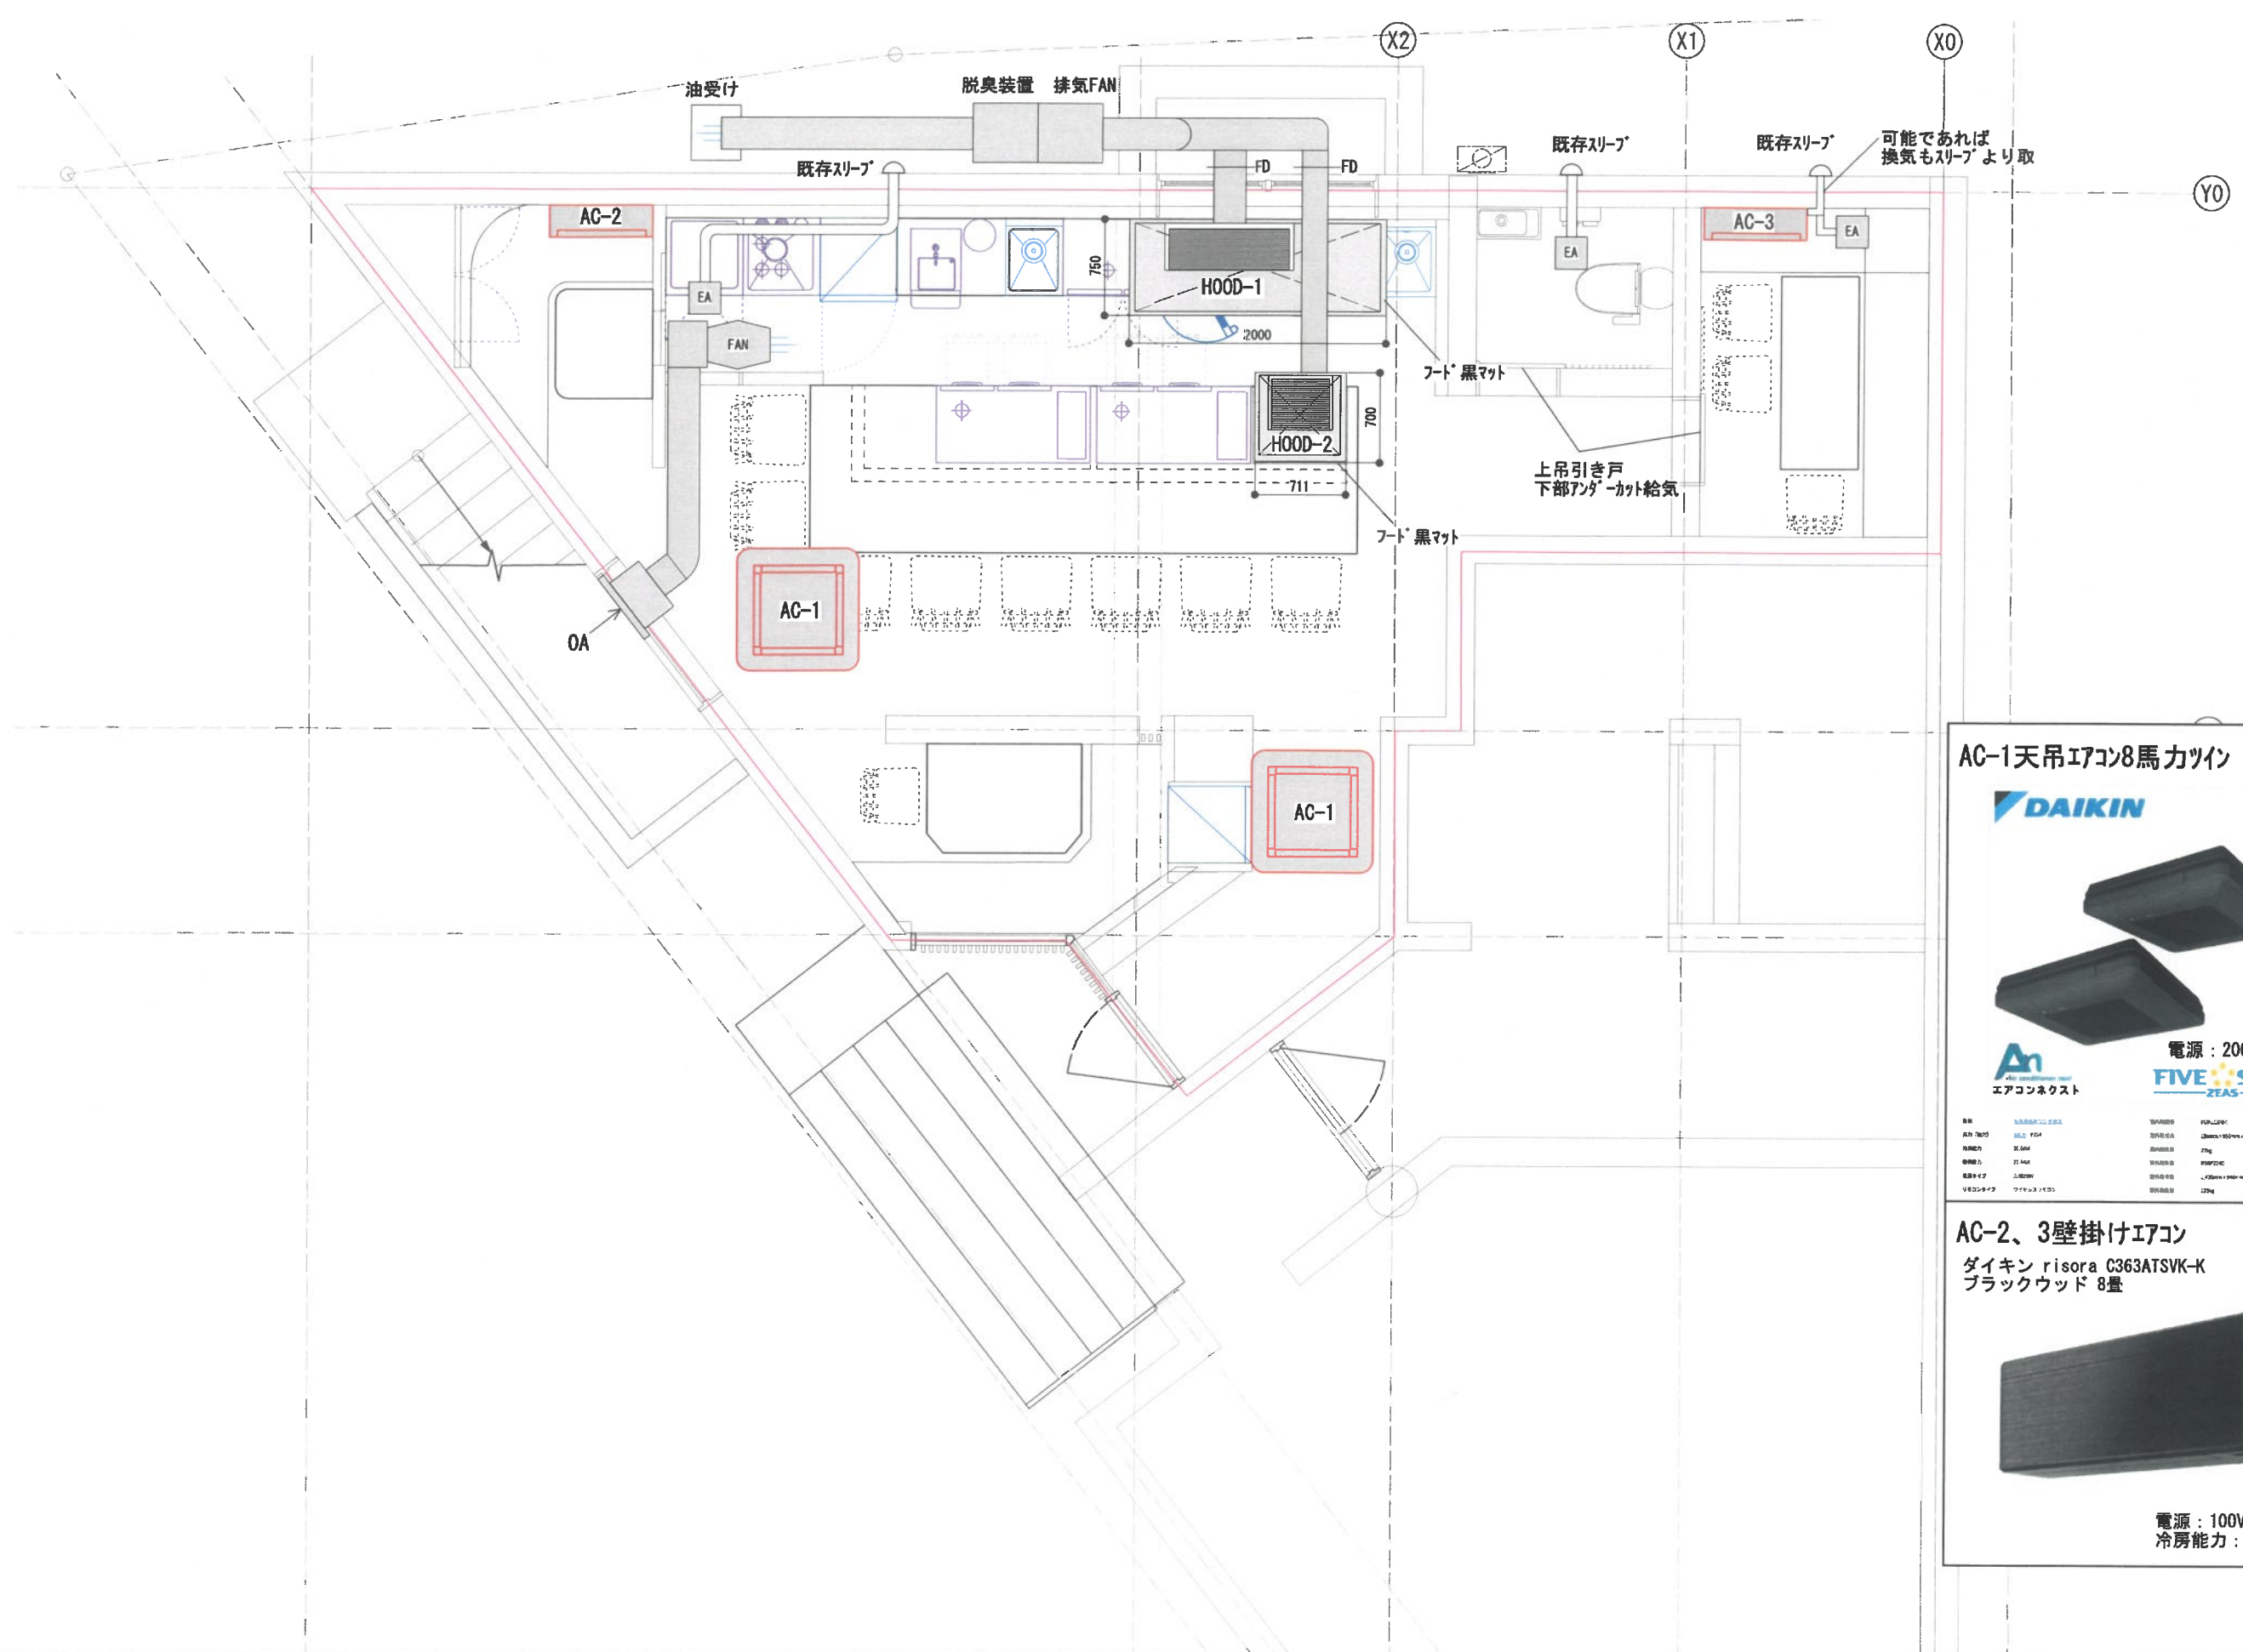

AC-1天吊エアコン8馬力ツイン

DAIKIN

電源 : 200V 6.95KW

An
エアコンネクスト

品名	天吊型エアコン	型式	FUJ28PC1
冷房能力	28.0kW	冷房能力	28.0kW
電圧	200V	電圧	200V
電源タイプ	三相200V	電源タイプ	三相200V
重量	120kg	重量	120kg

AC-2、3壁掛けエアコン

ダイキン risora C363ATSVK-K
ブラックウッド 8畳

電源 : 100V 1.15KW
冷房能力 : 0.59kW

① カウンターチェア 8脚
MYC1330GY スチール椅子
W565×D550×H745 (SH460 AH710)



② チェア 4脚 W350×D350×H400
Dice Stool
Shop
FLYME Parlor / フライミーパーラー
Brand
SWITCH / スウィッチ



座：ビニールレザー

A ベンチソファ



背：ファブリック
座：ビニールレザー 台下収納

a テーブル W750×D850×H750
T=50mm



天板：木下地 モルテックス仕上
脚：スチール黒 アジャスター付

b テーブル W1200×D850×H750
T=50mm





天板：木下地 モルテックス仕上
脚：スチール黒 アジャスター付

c テーブル W1700×D600×H750
T=50mm



天板：木下地 モルテックス仕上
脚：スチール黒 アジャスター付

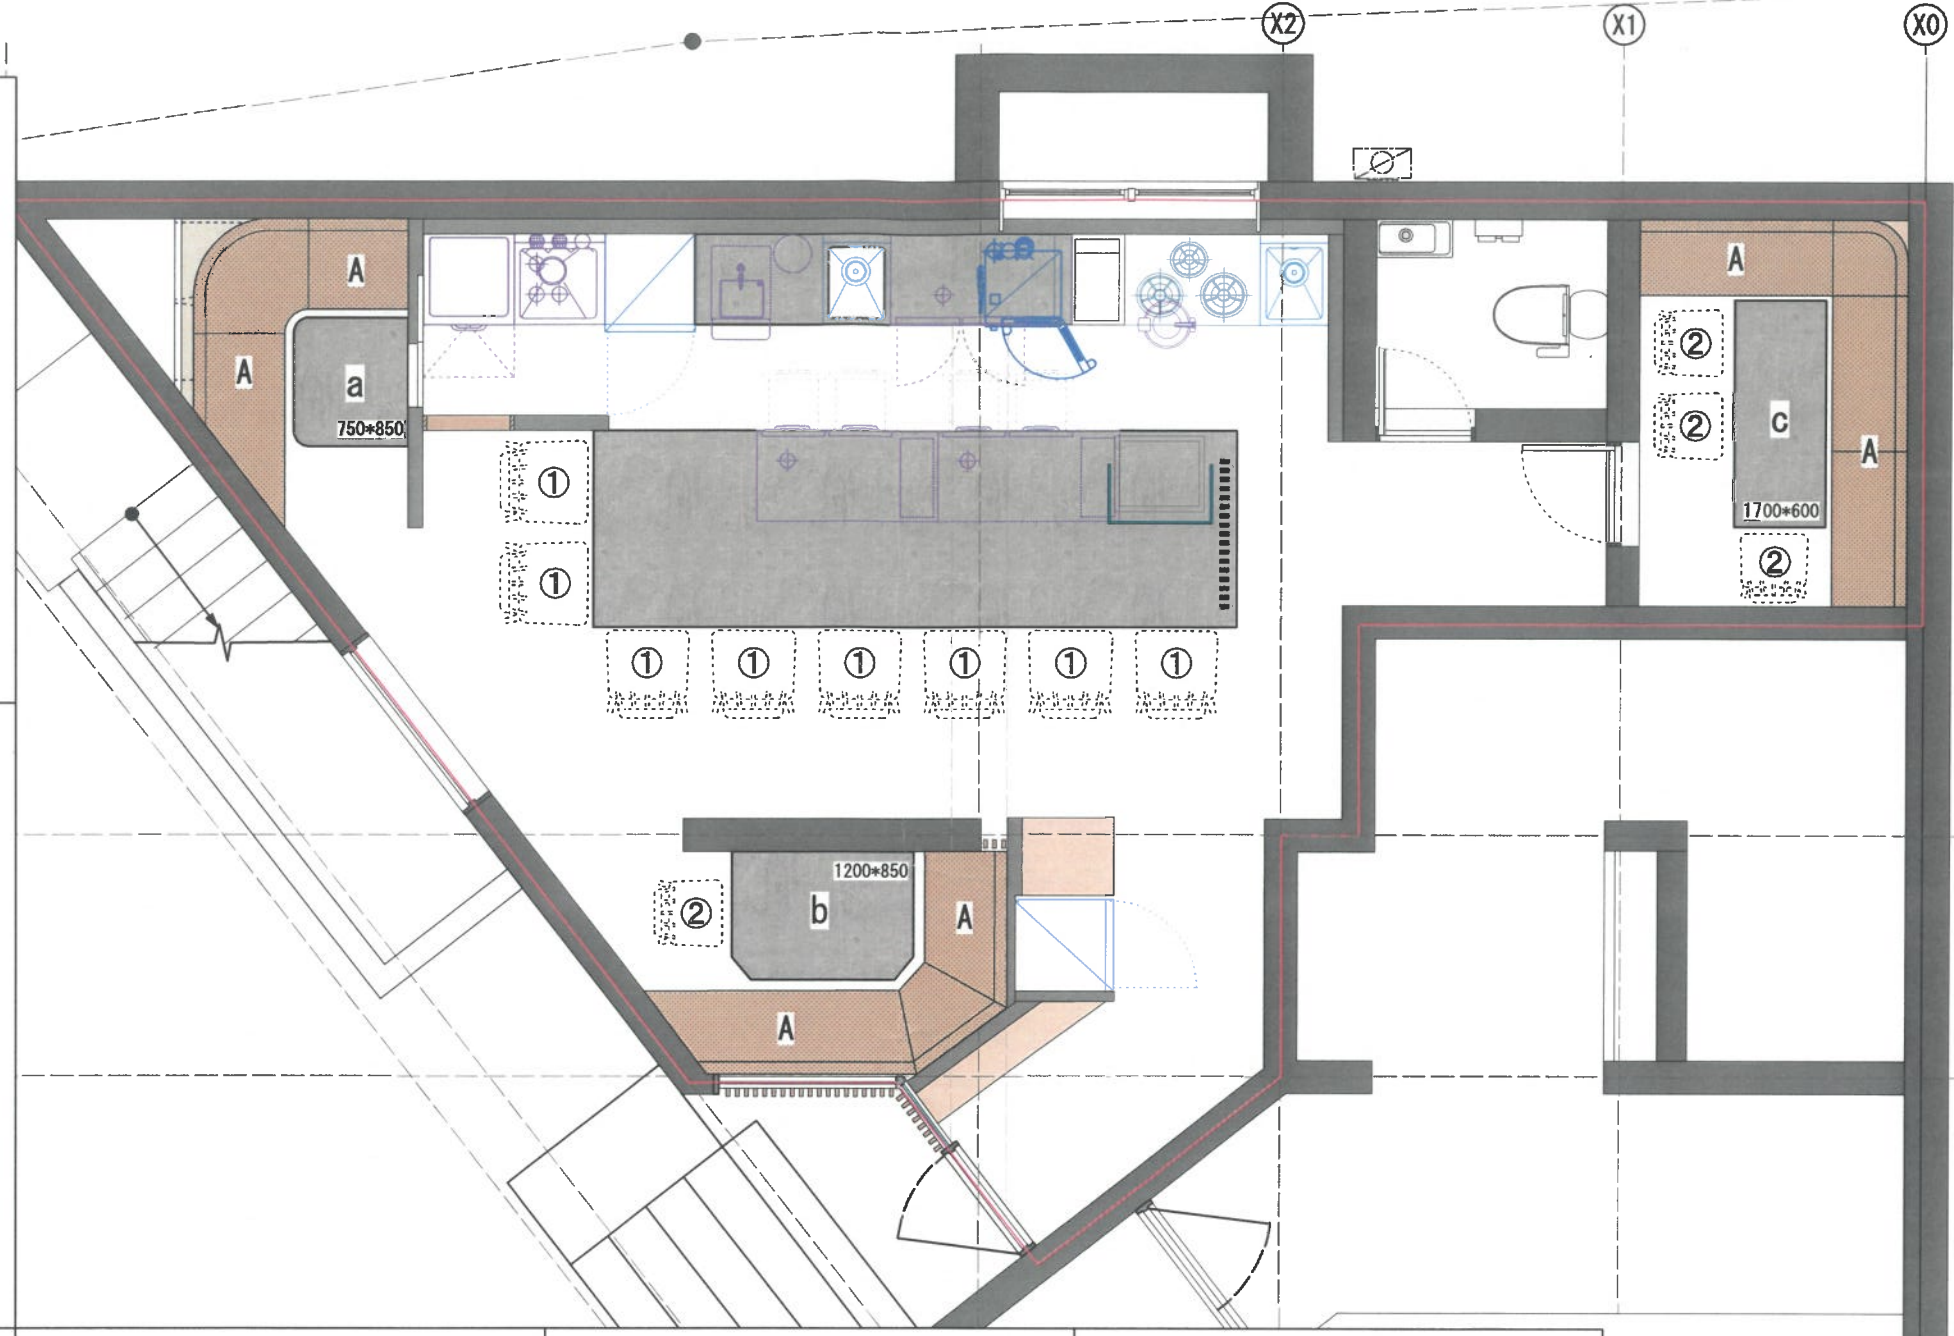

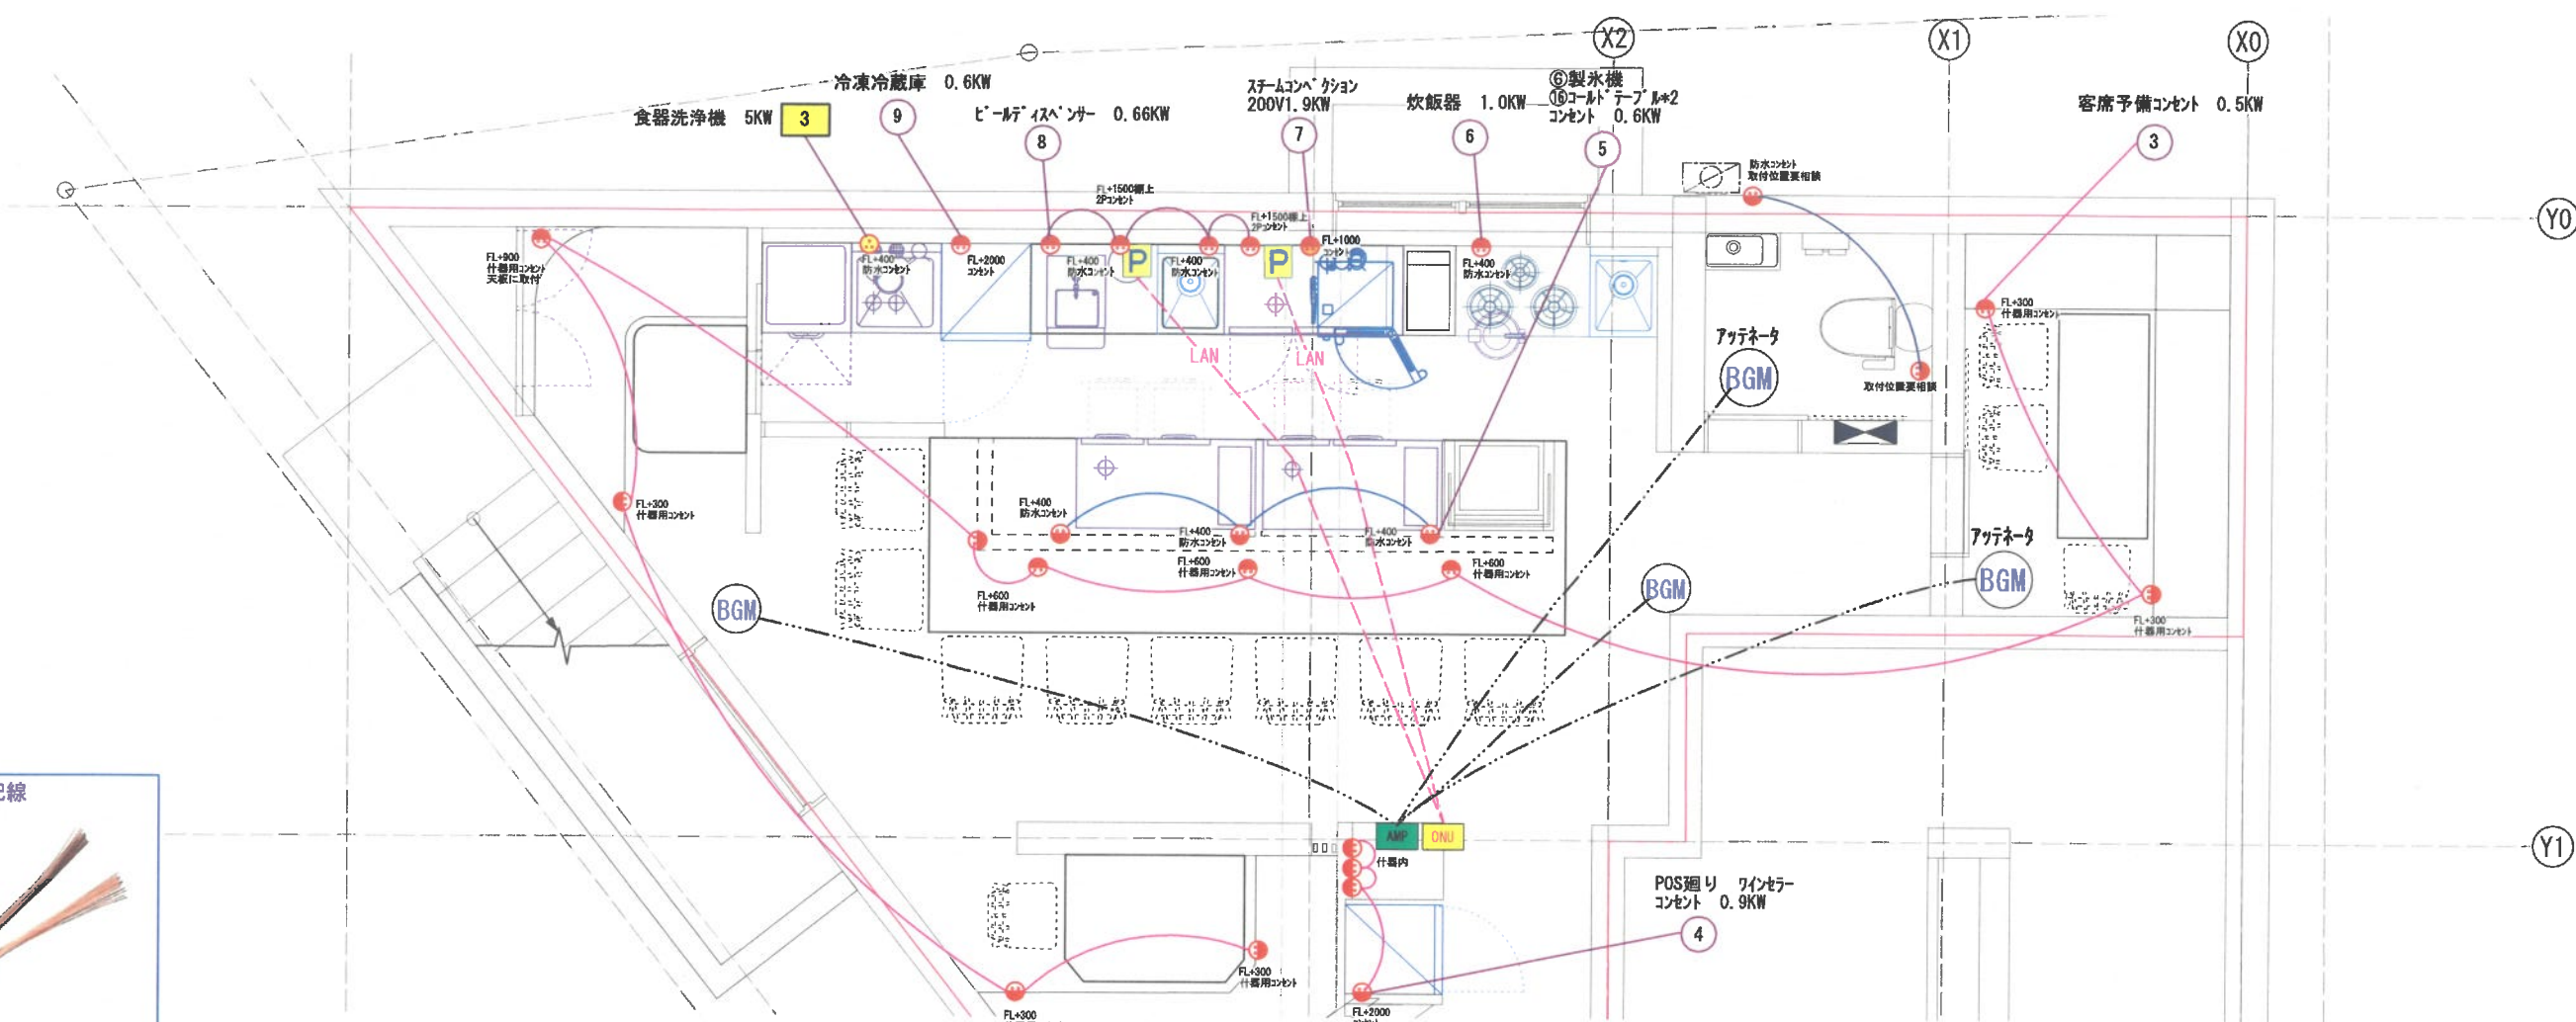

使用スピーカー配線



0.18mmx30芯、0.75mm2

使用LAN配線 CAT6A



CAT6の2倍の帯域幅を実現！
超高速10Gbps LANケーブル

各プリンター側には差込口
プラグを取付下さい。

使用BGM機材
内装工事お見積りにお含み下さい。

露出スピーカー 4台
オボックススピーカー ブラック
【AV-6351IMP-B】

スピーカーハンガー ブラック 4台

BGMアンプ 1台
卓上型コンパクトアンプ
【BC-20】UNI-PEX

Bluetooth オーディオレシーバー
【LBT-AVWAR501BK】 ELECOM

電灯割当想定
10KVA ≥ 8.54KVA OK

1φ3W100/200V					
主開閉器 MCB 50A 誘導灯					
0.8	照明	1	2	換気扇	0.5
0.5	店内予備コンセント	3	4	POSコンセント	0.8
0.6	⑥製氷機 ⑩コールドテーブル*2	5	6	炊飯器	1.0
1.9	スチームコンベクション	7	8	ビールディスプレイ	0.66
0.6	冷凍冷蔵庫	9	10	壁掛けエアコン	0.59
0.59	壁掛けエアコン	11	12	予備	
	予備	13	14	予備	

3φ 3W200V

動力割当 (想定)
17KW ≧ 15.15KW OK

15.15KW

主開閉器
MCB
50A

Diagram illustrating a 3-phase 3-wire 200V power distribution system. The main circuit breaker (MCB 50A) is connected to a vertical busbar. The busbar is divided into six sections, each with an ELB (Earth Leakage Breaker) and a 30A/20A rating. The sections are labeled 1 through 6.

Section	Equipment	Quantity	Notes
1	ツインエアコン	1	
2	排気ファン	2	想定
3	①. 食器洗浄機	1	
4	給気ファン	1	想定
5			
6			

